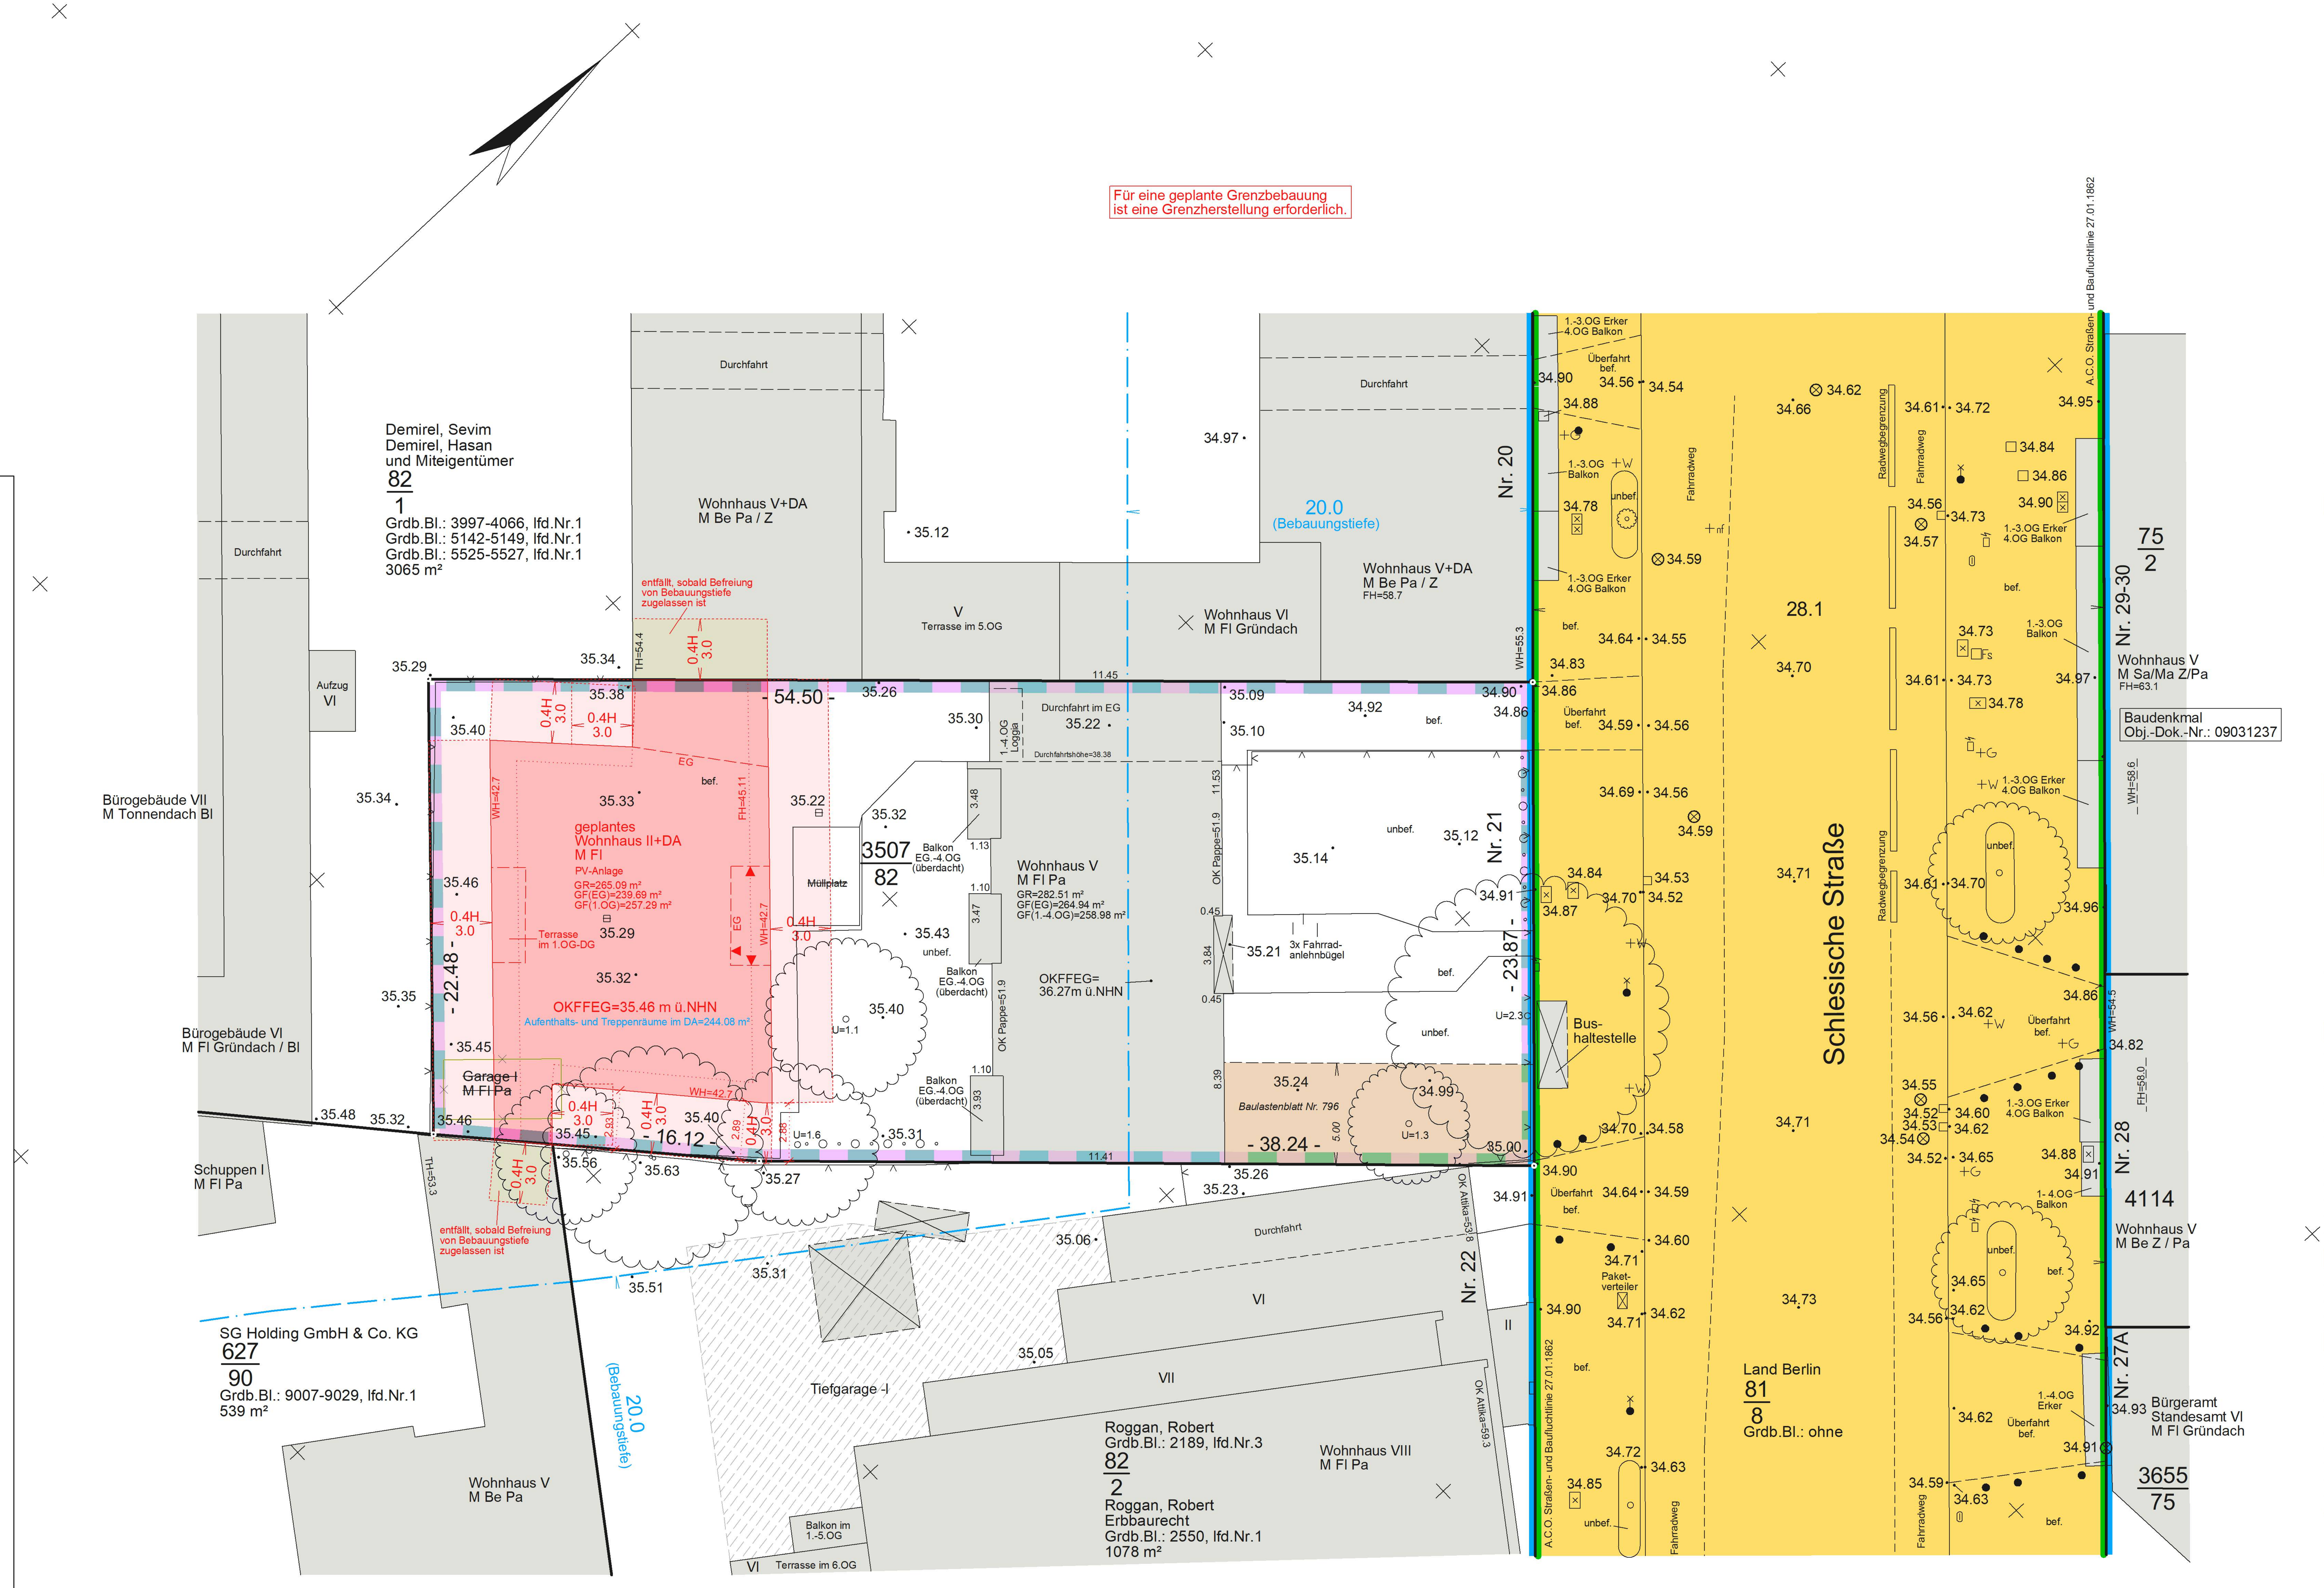
Für eine geplante Grenzbebauung ist eine Grenzherstellung erforderlich.
Demirel, Sevim
Demirel, Hasan
und Miteigentümer
82/1
Grdb.Bl.: 3997-4066, lfd.Nr.1
Grdb.Bl.: 5142-5149, lfd.Nr.1
Grdb.Bl.: 5525-5527, lfd.Nr.1
3065 m²
Durchfahrt
Wohnhaus V+DA
M Be Pa / Z
V
Terrasse im 5.OG
Wohnhaus VI
M Fl Gründach
Wohnhaus V+DA
M Be Pa / Z
FH=58.7
20.0
(Bebauungstiefe)
Nr. 20
Nr. 21
Nr. 22
Aufzug
VI
Bürogebäude VII
M Tonnendach Bl
Bürogebäude VI
M Fl Gründach / Bl
Schuppen I
M Fl Pa
entfällt, sobald Befreiung von Bebauungstiefe zugelassen ist
0.4H
3.0
- 54.50 -
- 22.48 -
- 16.12 -
- 23.87 -
- 38.24 -
geplantes
Wohnhaus II+DA
M Fl
PV-Anlage
GR=265.09 m²
GF(EG)=239.69 m²
GF(1.OG)=257.29 m²
Terrasse im 1.OG-DG
OKFFEG=35.46 m ü.NHN
Aufenthalts- und Treppenräume im DA=244.08 m²
~~Garage I~~
~~M Fl Pa~~
~~Müllplatz~~
3507/82
Balkon EG.-4.OG (überdacht)
Wohnhaus V
M Fl Pa
GR=282.51 m²
GF(EG)=264.94 m²
GF(1.-4.OG)=258.98 m²
OKFFEG=
36.27m ü.NHN
Durchfahrt im EG
1.-4.OG Loggia
Durchfahrtshöhe=38.38
3x Fahrrad-anlehnbügel
Baulastenblatt Nr. 796
unbef.
bef.
SG Holding GmbH & Co. KG
627/90
Grdb.Bl.: 9007-9029, lfd.Nr.1
539 m²
Wohnhaus V
M Be Pa
Tiefgarage -I
Balkon im 1.-5.OG
VI Terrasse im 6.OG
VI
VII
II
Wohnhaus VIII
M Fl Pa
Roggan, Robert
Grdb.Bl.: 2189, lfd.Nr.3
82/2
Roggan, Robert
Erbbaurecht
Grdb.Bl.: 2550, lfd.Nr.1
1078 m²
OK Attika=53.8
OK Attika=59.3
Schlesische Straße
28.1
Land Berlin
81/8
Grdb.Bl.: ohne
Fahrradweg
Radwegbegrenzung
Bus-haltestelle
Paket-verteiler
Überfahrt bef.
1.-3.OG Erker 4.OG Balkon
1.-3.OG Balkon
A.C.O. Straßen- und Baufluchtlinie 27.01.1862
Nr. 29-30
75/2
Wohnhaus V
M Sa/Ma Z/Pa
FH=63.1
Baudenkmal
Obj.-Dok.-Nr.: 09031237
WH=58.6
Nr. 28
4114
Wohnhaus V
M Be Z / Pa
WH=54.5
FH=58.0
Nr. 27A
Bürgeramt
Standesamt VI
M Fl Gründach
3655/75
1.-4.OG Erker
1- 4.OG Balkon

Legende

▨	bestehende Bebauung	━	Flurstücksgrenze	☒ □ ⊗	Kabel- / eckiger / runder Schacht
🟥	geplante Bebauung	━	geplante Teilungsgrenze	⊖ □ϟ ●	Hydrant / Verteilerkasten / Poller
┆	bestehende Abstandsfläche	━○━	Grenzpunkt / mit Abmarkung	+W+G+nf	Wasser- / Gas- / unbekannter Schieber
┆	geplante Abstandsfläche	━ ⋯	Flurgrenze	⊟	Regenwassereinlauf (Gully)
🟨	öffentliche Verkehrsfläche	╳	zu beseitigende Anlage	◀	Lichtschacht / Hauseingang
🟫	Baulastfläche		Mauer / Stützmauer	U=1.6	Laub- / Nadelbaum, Krone maßstäblich
☒	Überdachung		Zaun		Gebüsch / oberirdischer Hydrant
		○ ∘ ○	Hecke		Laterne / Fahrleitungs- / Fahnenmast
			Geländer		
			Ablaufrinne		
			Böschung		

• 55.83	Geländehöhe
• (55.83)	interpolierte Höhe
• [55.83]	geplantes Geländeniveau
- 55.83 -	Grenzlänge
55.83	Bestimmungsmaß
(55.8)	grafisch ermitteltes Maß
[55.83]	berechnetes Maß

M/H	Massiv- / Holzbau
Whs/Schp	Wohnhaus / Schuppen
Wi	Wirtschaftsgebäude
DA/SG	Dachausbau / Staffelgeschoss
Pu/Sa/Ze	Pult- / Sattel- / Zeltdach
Fl/Ma/Be	Flach- / Mansarden- / Berliner Dach
Wa/Kwa	Walm- / Krüppelwalmdach
Pa/Et/Z/Bl	Pappe / Eternit / Ziegel / Blech
FH/WH	First- / Wandhöhe
TH/BWH	Trauf- / Brandwandhöhe

━	Baulinie
━	Baugrenze oder Baufluchtlinie
━	Straßenbegrenzungs- oder Straßenfluchtlinie
╍	Baugrundstücksbegrenzung
╍	Grundstücksgrenze (Buchgrundstück)

Bauaufsichtliche Sichtvermerke

Öffentlich bestellte Vermessungsingenieure
Beratende Ingenieure
Storkower Straße 101 B, 10407 Berlin
Tel. 030 4284130, Fax 030 42841329, post@biermann-heldt.de

BIERMANN HELDT

Lageplan Berlin - Kreuzberg
Schlesische Straße 21

Lageplan zur Bauanfrage

0 1 2 5 10 20 m
Maßstab 1:200

Bezirk Friedrichshain-Kreuzberg		Geschäftszeichen
Lagebezug Soldner-Berlin Höhenbezug DHHN2016	Blatt 1 von 1 420 x 780	12-063-0

Katasternachweis für das Baugrundstück vom 19.11.2024

Gemarkung	Flur	Flurstück	Grdb.Bl.	lfd.Nr.	Fläche	Eigentümer
Kreuzberg	1	3507/82	3594	1	1287 m²	"GbR Schlesische Str. 21"

Planungsrechtliche Bestimmungen

Rechtsgrundlage	BO 58/Baunutzungsplan, Baustufe V/3	Art der Nutzung	gemischtes Gebiet
Maß der Nutzung	GRZ 0.3, 5 Vollgeschosse (GFZ 1.5), Bebauungstiefe 20 m	Bauweise	geschlossen

Nutzungsberechnung siehe Anlage

Bearbeitungsverlauf

a	30.08.2024	örtliche Messung (99 131)	Brambati
b	11.09.2024	Planfertigung	Brambati
c	24.09.2024	Baulasteintrag nach Erhalt der Auskunft	Urbanski
d	28.11.2024	Projekteintrag nach Planunterlagen vom 19.09.2024, Architekt Jörn Nolte	Khabbazian

Allgemeine Hinweise

Angefertigt nach amtlichen Unterlagen und örtlicher Messung.

Grundstücksgrenzen und baurechtliche Linien sind nach Katasterunterlagen und planungsrechtlichen Bestimmungen vermaßt. Für genaue Maßangaben ist eine örtliche Grenzherstellung oder Absteckung der baurechtlichen Linien erforderlich. Für den Neubau ist nach Fertigstellung eine Gebäudevermessung gemäß § 19 Abs. 2 VermGBln durchzuführen. Der Lageplan enthält keine unterirdischen Leitungen.

Der Plan ist urheberrechtlich geschützt. Vervielfältigung verboten!

Ich übernehme die Verantwortung für die Richtigkeit:
Berlin, 28.11.2024

Dipl.-Ing. Jörg Biermann