


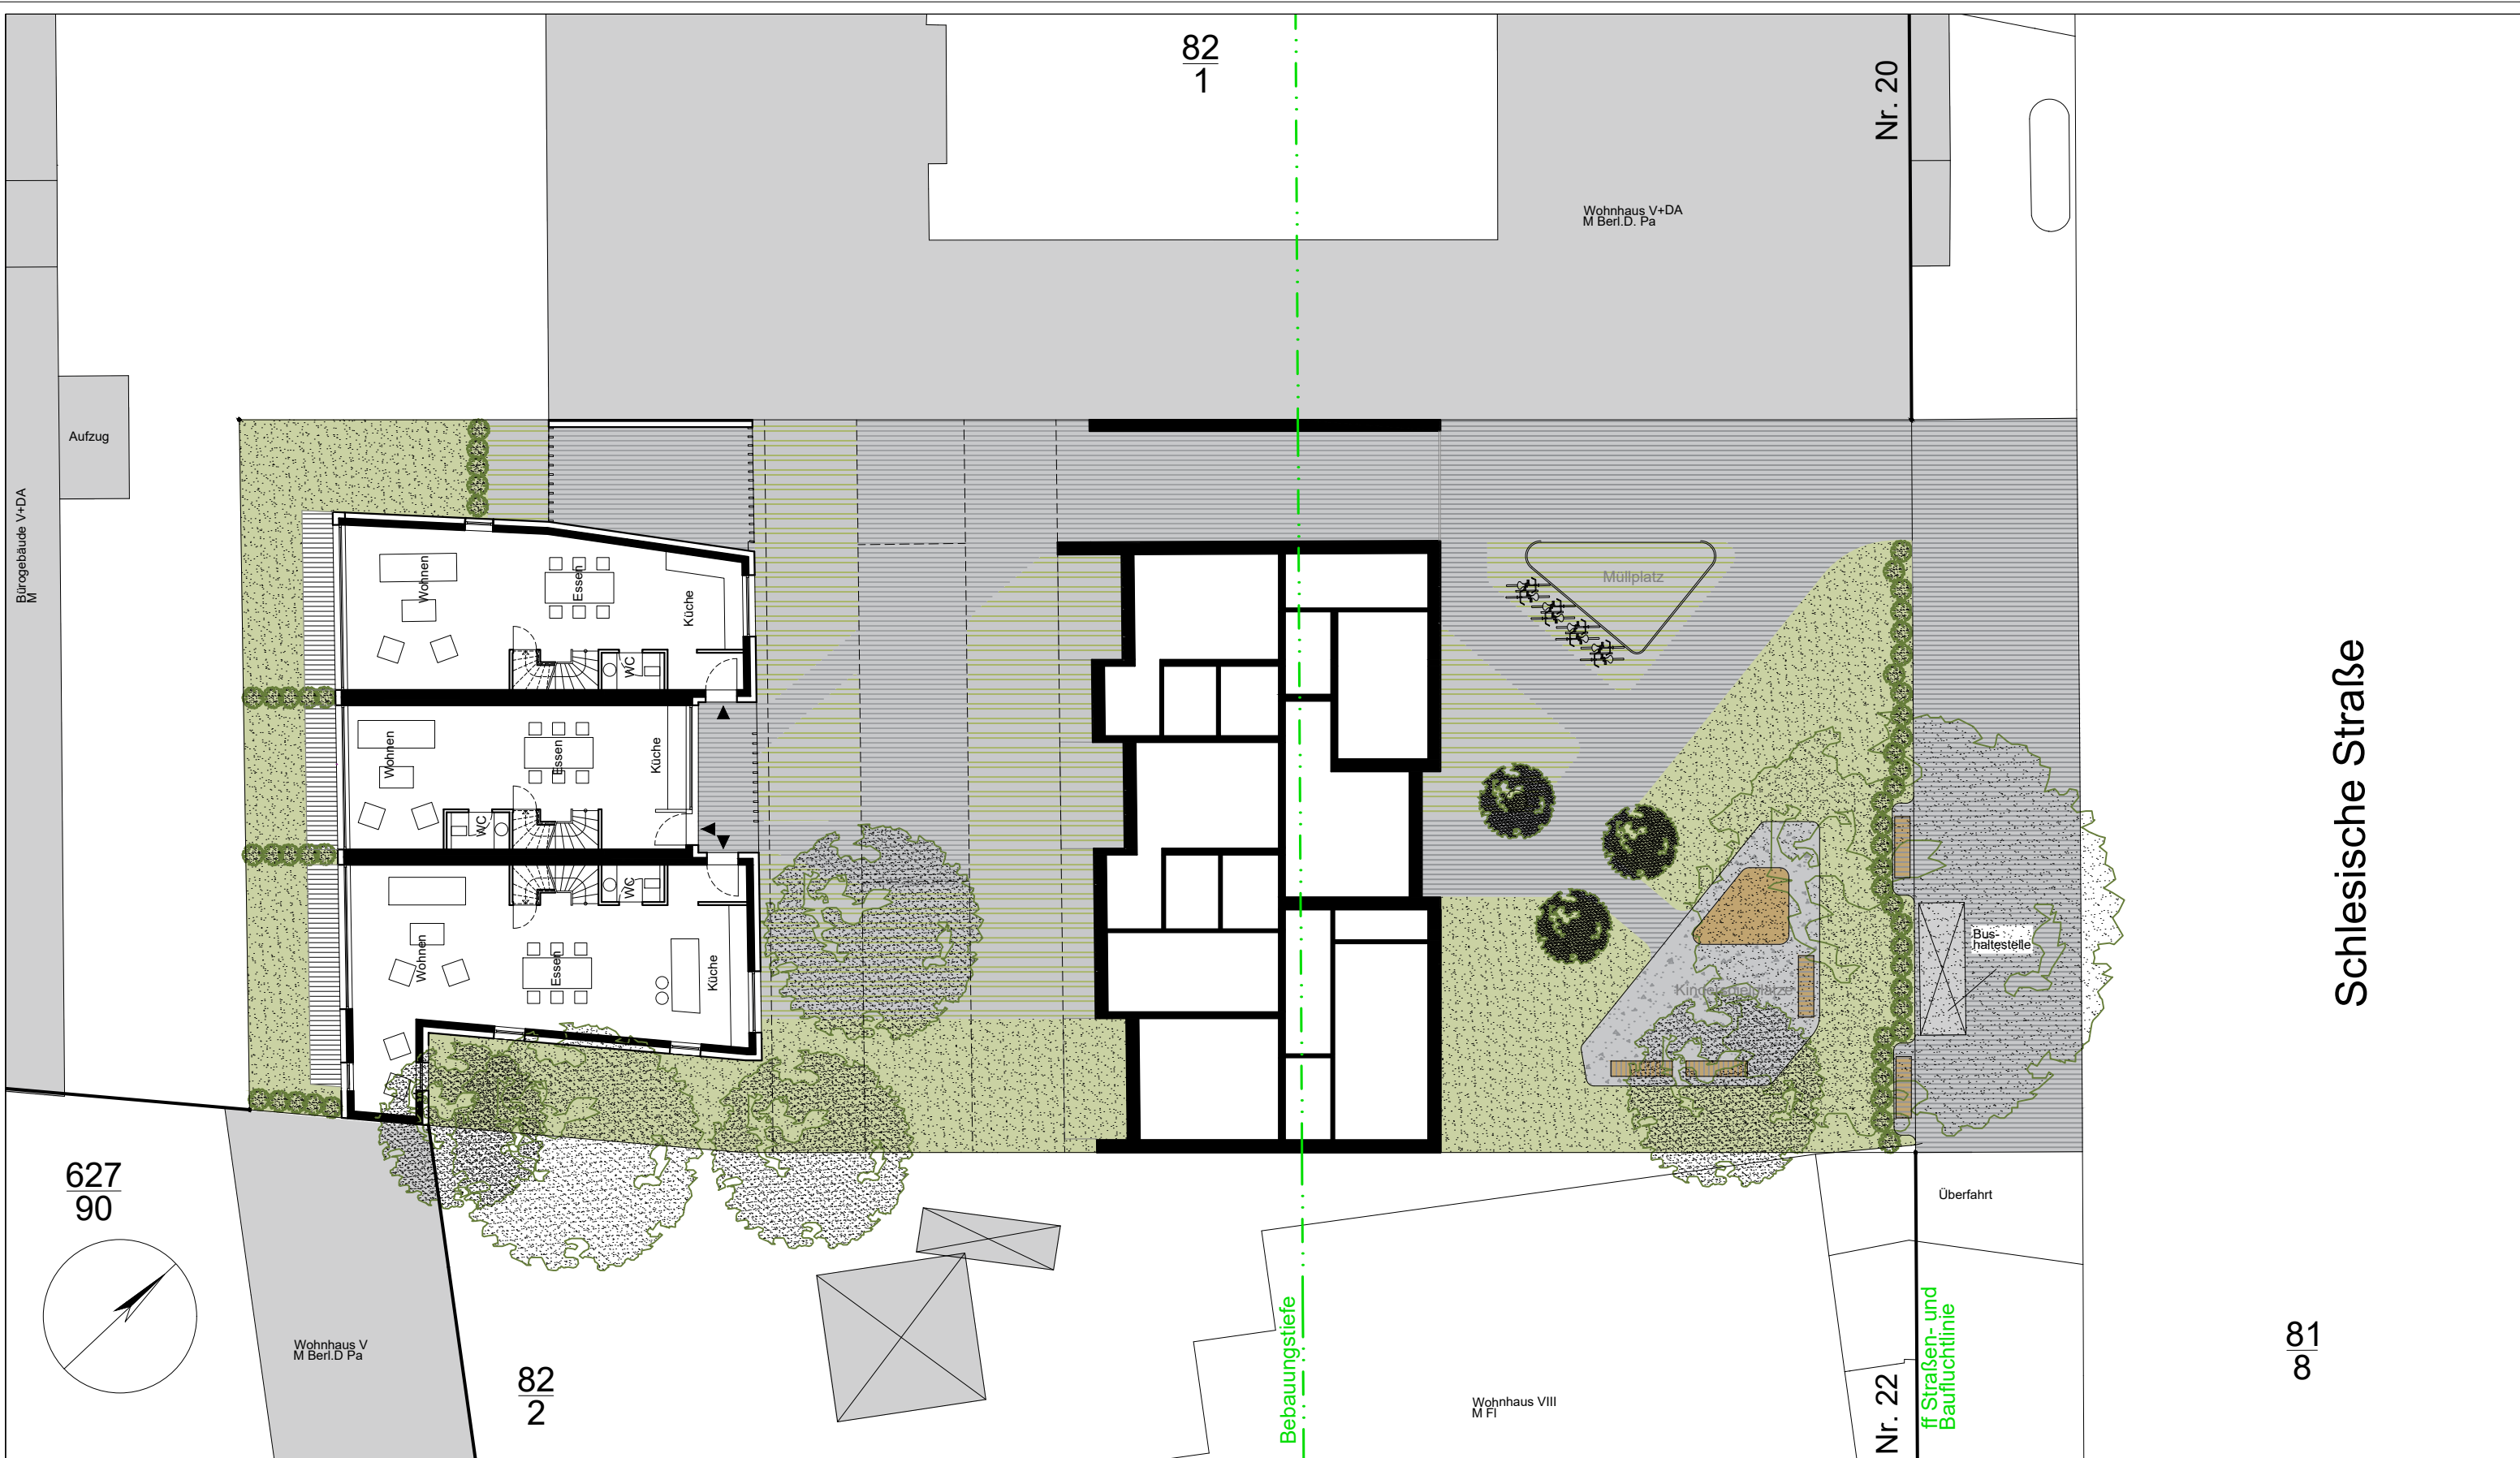

Höhensystem: DHHN 2016

± 0,00 m (± 0,00 = + 35,21m ü DHHN2016)
Schnittebene auf 1,0 m über Oberkante Fußboden.
Alle Flächen- und Umfangsberechnungen beziehen sich auf Rohbaumaße.
Brüstungshöhen sind von OKFF bis OK Rohbrüstung angegeben.
Höhen von Unter-/Überzügen verstehen sich incl. Deckenstärke, wenn nicht anders angegeben.

PLAN NICHT ZUM BAU FREIGEgeben

Adresse Bauvorhaben

Schlesische Str. 21
10997 Berlin

Adresse Bauherr	
-----------------	--

GbR Schlesische Str. 21
Moshe Kline
Schlesische Str. 21
10997 Berlin

Unterschrift Bauherr	
----------------------	--

Unterschrift und Stempel Architekt



S21	
-----	--

Bauvoranfrage

M 1:200


architactics
Jörn Nolte
10115 Berlin

ESSENZ Architecture Cai und Gärtner GbR
Esmarchstraße 3
10407 Berlin


Objektbezogener Lageplan

DIN A3


20.12.2024

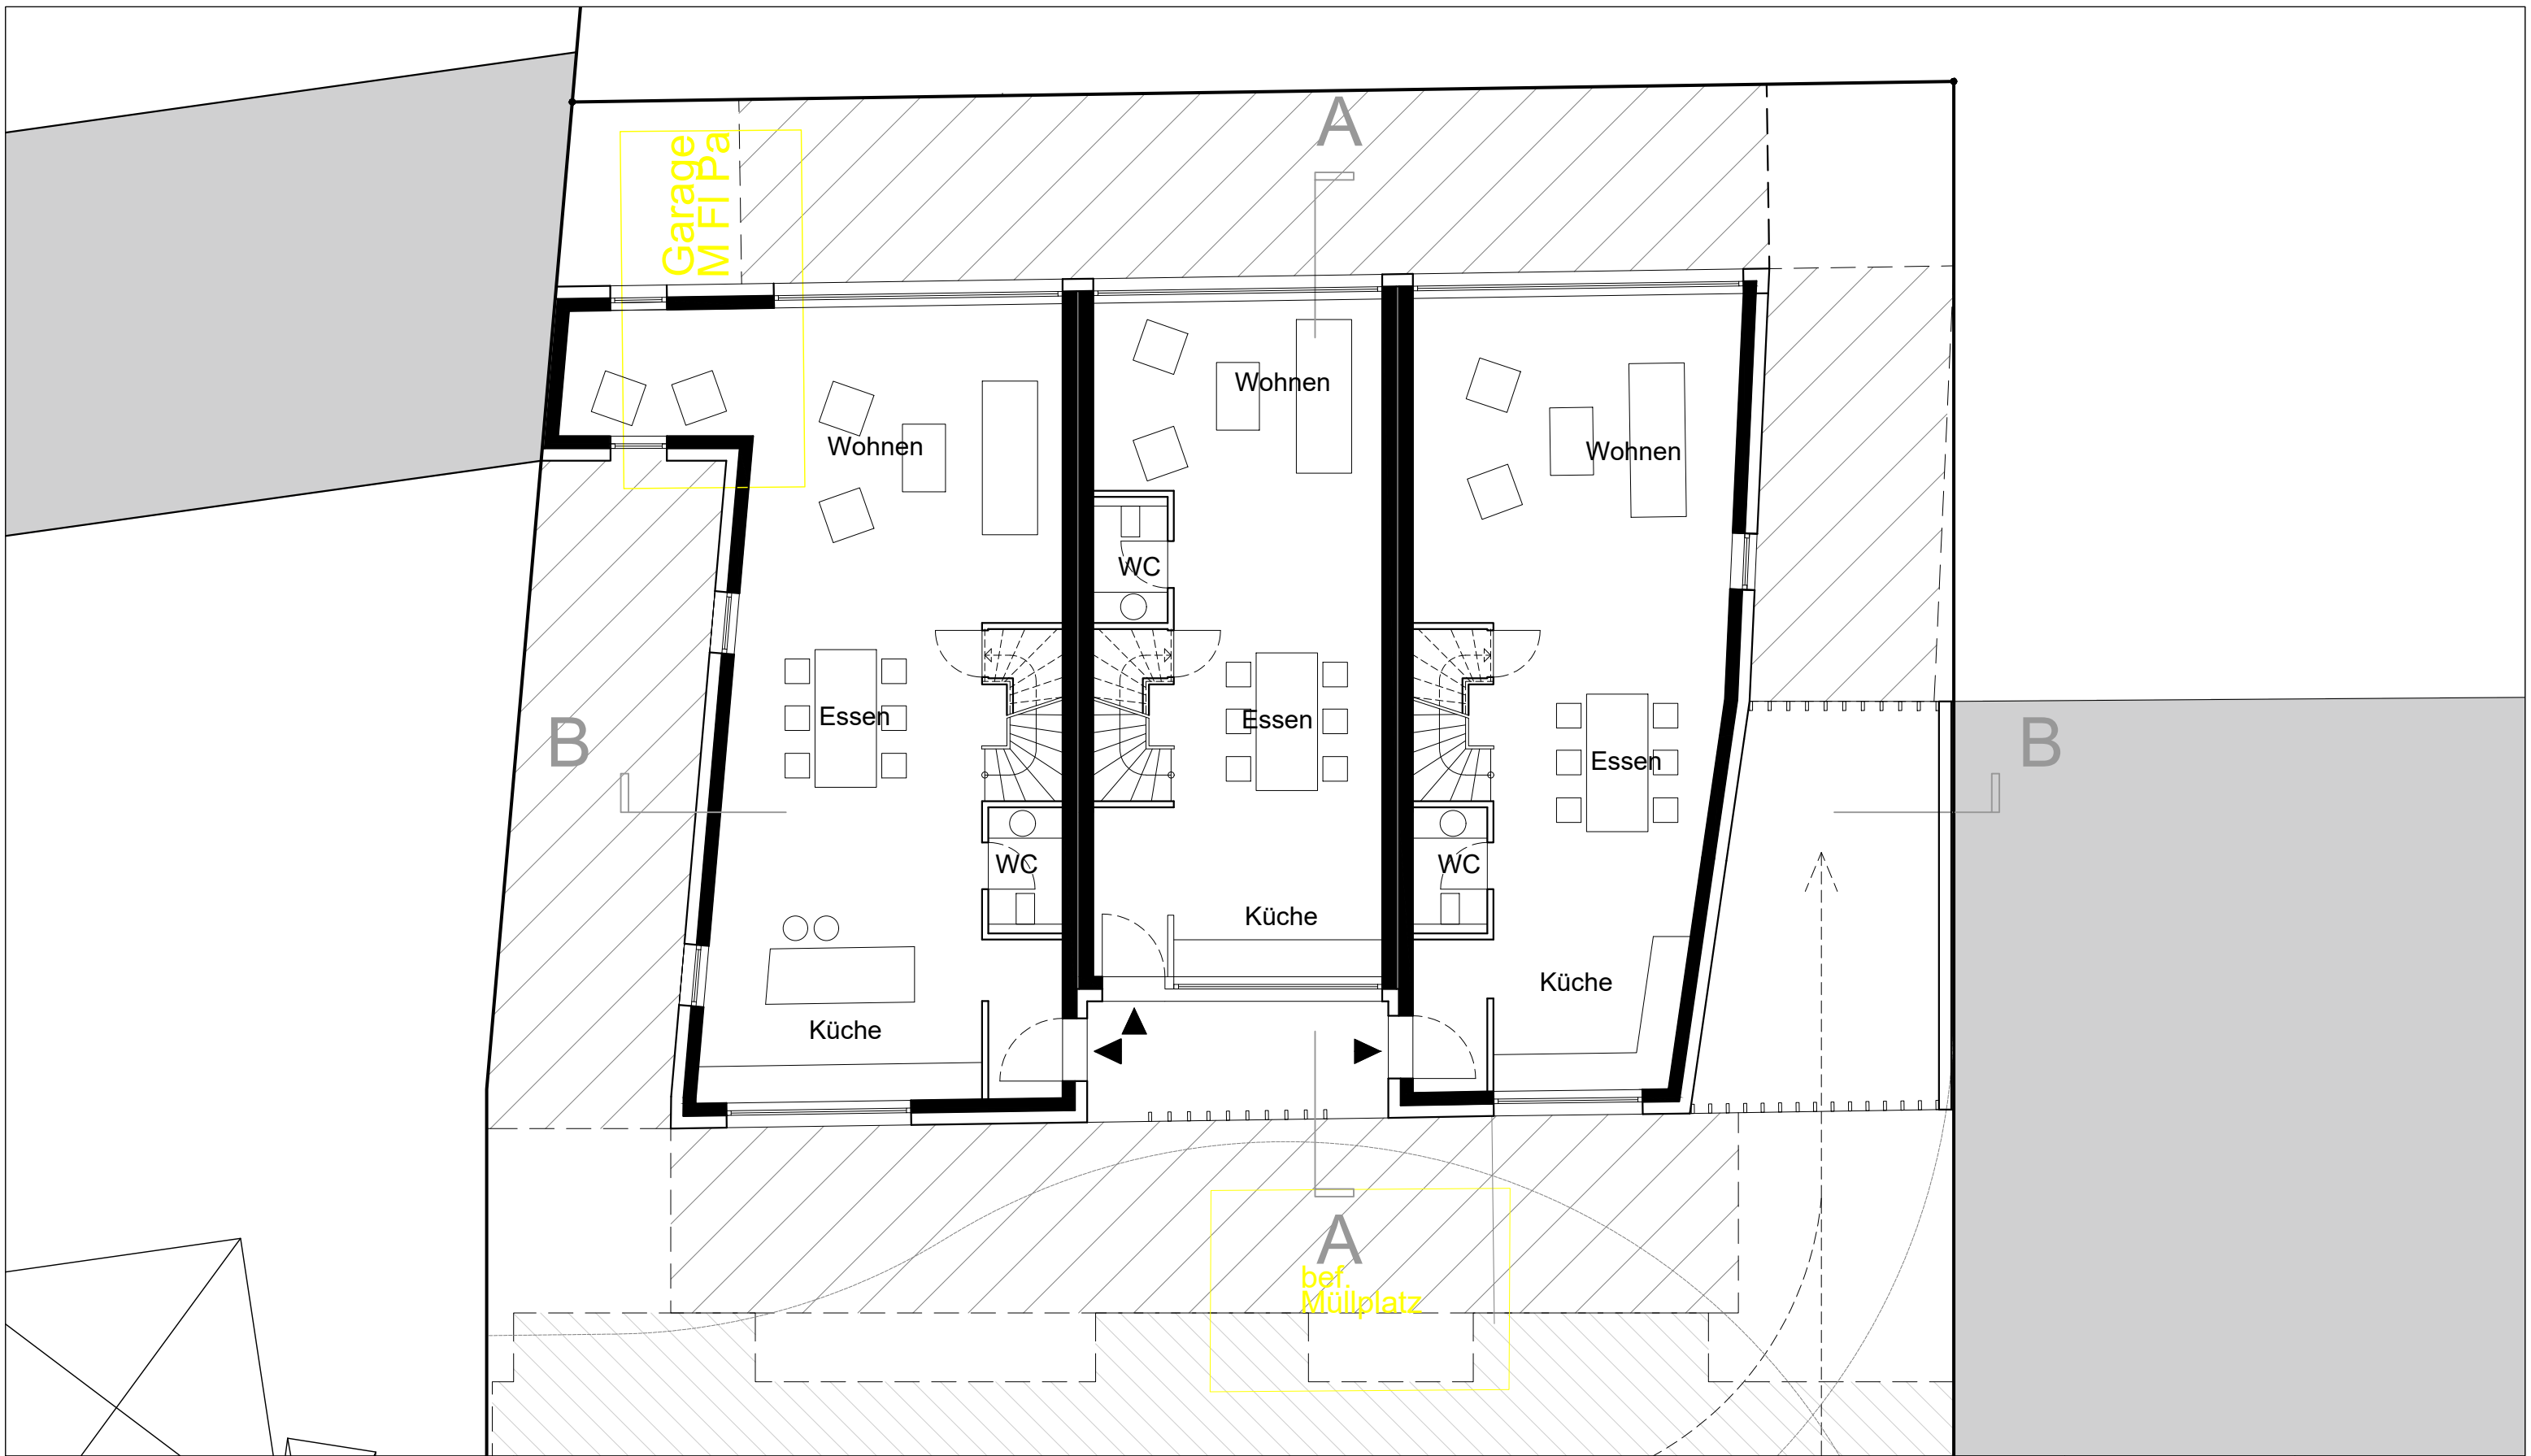


± 0,00 m (± 0,00 = + 35,21m ü DHHN2016) Schnittebene auf 1,0 m über Oberkante Fußboden. Alle Flächen- und Umfangsberechnungen beziehen sich auf Rohbaumaße. Brüstungshöhen sind von OKFF bis OK Rohbrüstung angegeben. Höhen von Unter-/Überzügen verstehen sich incl. Deckenstärke, wenn nicht anders angegeben. PLAN NICHT ZUM BAU FREIGEgeben	Adresse Bauvorhaben		Adresse Bauherr		Unterschrift Bauherr		Unterschrift und Stempel Architekt		S21	Townhouses - Erdgeschoss	
	Schlesische Str. 21 10997 Berlin		GbR Schlesische Str. 21 Moshe Kline Schlesische Str. 21 10997 Berlin						Bauvoranfrage		
									M 1:100	DIN A3	20.12.2024
									architactics Jörn Nolte 10115 Berlin ESSENZ Architecture Cai und Gärtner GbR Esmarchstraße 3 10407 Berlin		

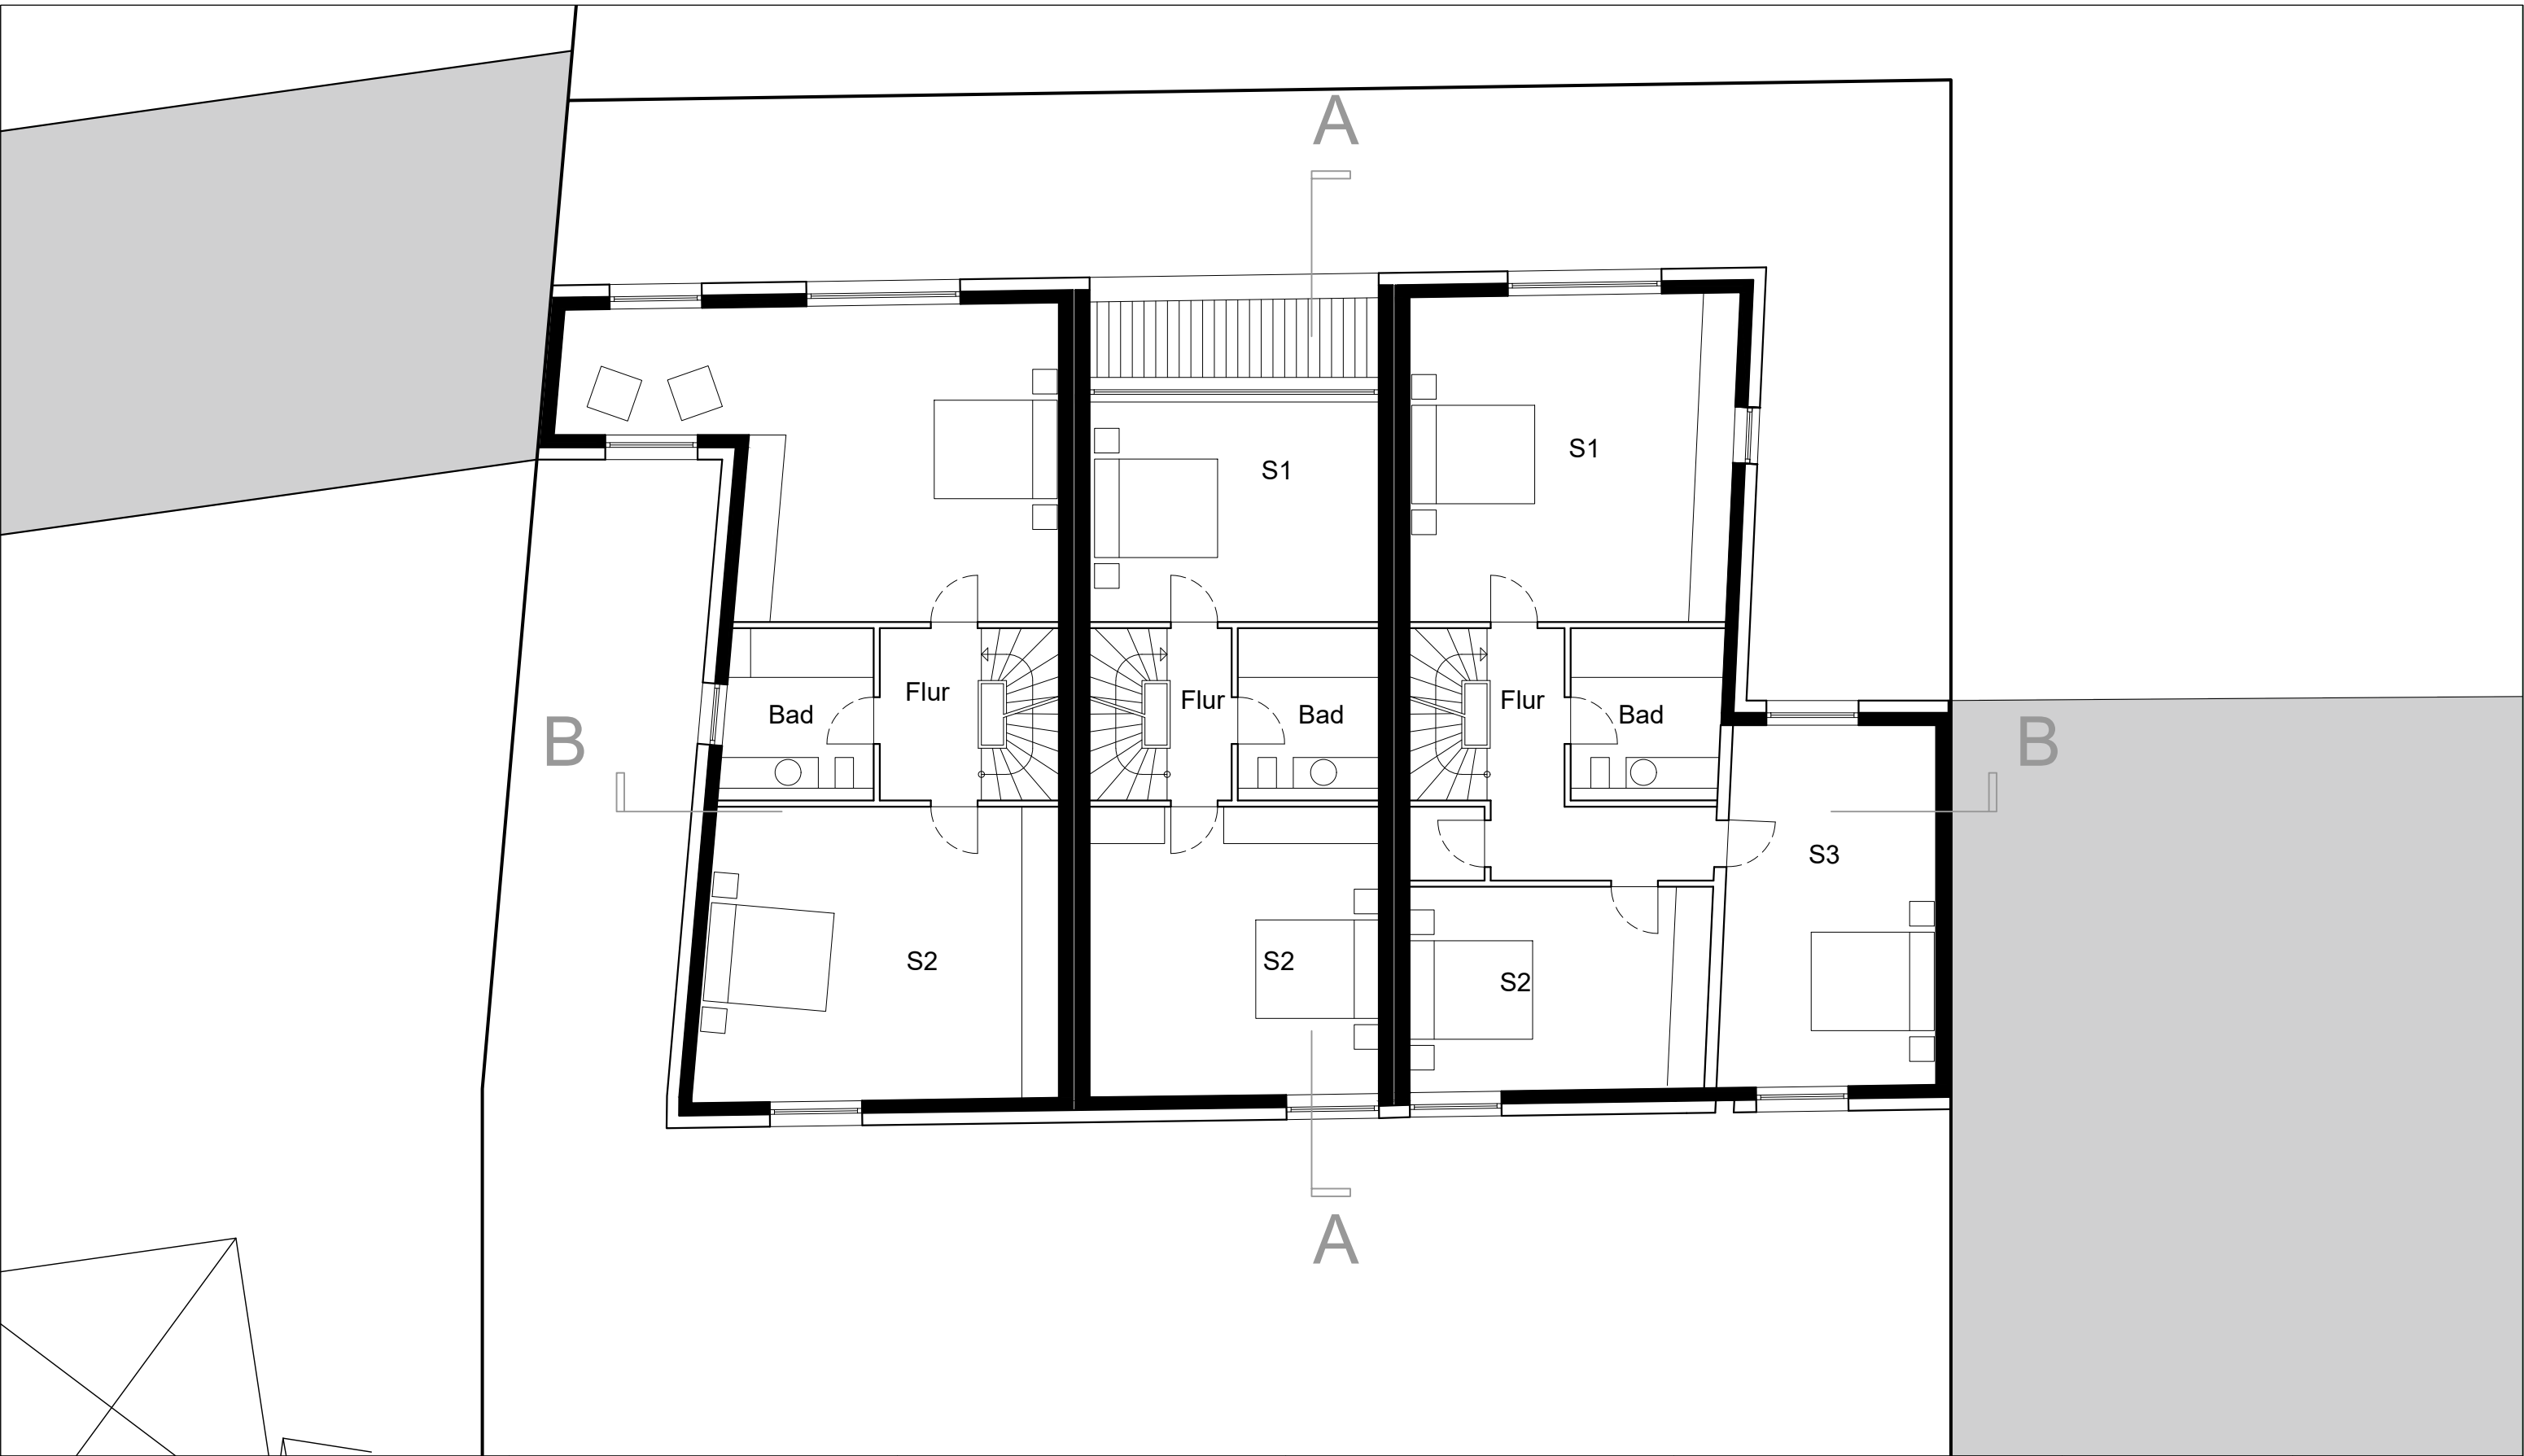


± 0,00 m (± 0,00 = + 35,21m ü DHHN2016) Schnittebene auf 1,0 m über Oberkante Fußboden. Alle Flächen- und Umfangsberechnungen beziehen sich auf Rohbaumaße. Brüstungshöhen sind von OKFF bis OK Rohbrüstung angegeben. Höhen von Unter-/Überzügen verstehen sich incl. Deckenstärke, wenn nicht anders angegeben. PLAN NICHT ZUM BAU FREIGEgeben	Adresse Bauvorhaben		Adresse Bauherr		Unterschrift Bauherr		Unterschrift und Stempel Architekt		S21	Townhouses - 1.Obergeschoss	
	Schlesische Str. 21 10997 Berlin		GbR Schlesische Str. 21 Moshe Kline Schlesische Str. 21 10997 Berlin						Bauvoranfrage		
									M 1:100	DIN A3	20.12.2024
									architactics Jörn Nolte 10115 Berlin ESSENZ Architecture Cai und Gärtner GbR Esmarchstraße 3 10407 Berlin		

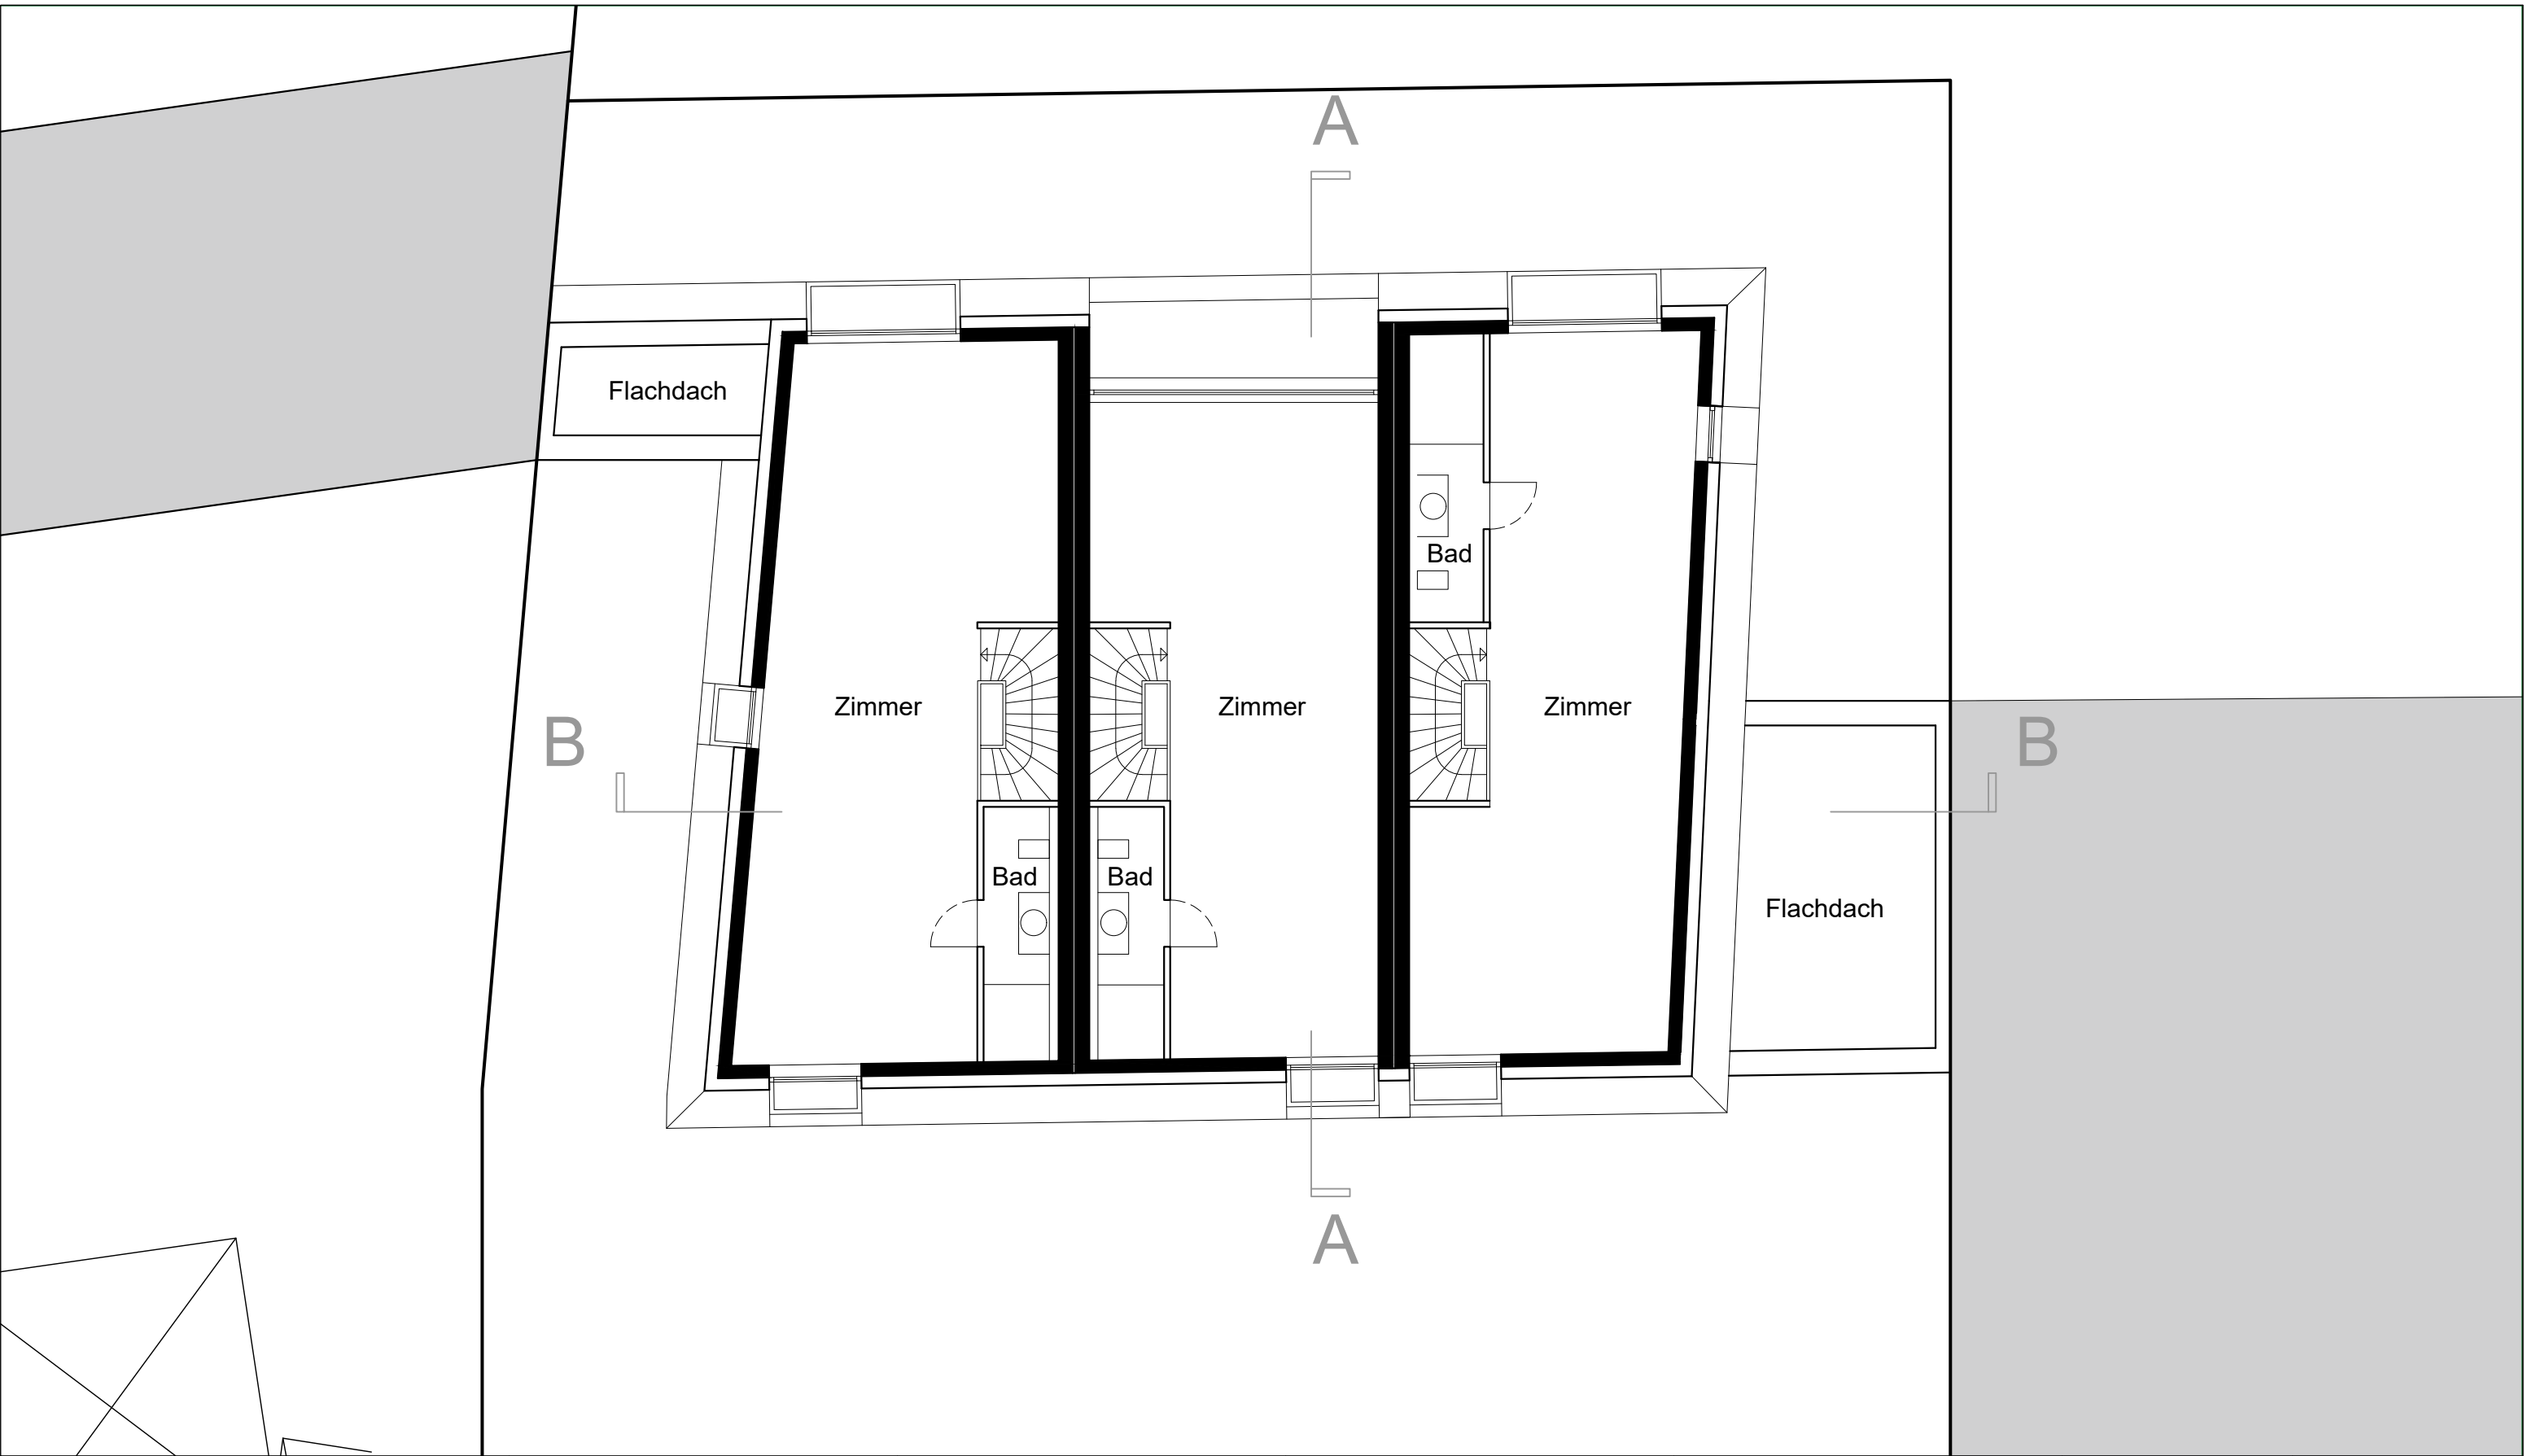

± 0.00 m (± 0.00 m ± 35.21 m ü DHHN 2016) Schnittebene auf 1.0 m über Oberkante Fußboden. Alle Flächen- und Umfangsberechnungen beziehen sich auf Rohbaumaße. Brüstungshöhen sind von OKFF bis OK Rohbrüstung angegeben. Höhen von Unter-/Überzügen verstehen sich incl. Deckenstärke, wenn nicht anders angegeben.	Adresse Bauvorhaben		Adresse Bauherr		Unterschrift Bauherr		Unterschrift und Stempel Architekt		S21	Townhouses - 2.Obergeschoss	
	Schlesische Str. 21		GbR Schlesische Str. 21						Bauvoranfrage		
	10997 Berlin		Moshe Kline						M 1:100	DIN A3	20.12.2024
	PLAN NICHT ZUM BAU FREIGEgeben		Schlesische Str. 21				Architektenliste Nr. 18211 Jörn Nolte Architekt		architactics Jörn Nolte 10115 Berlin ESSENZ Architecture Cai und Gärtner GbR Esmarchstraße 3 10407 Berlin		

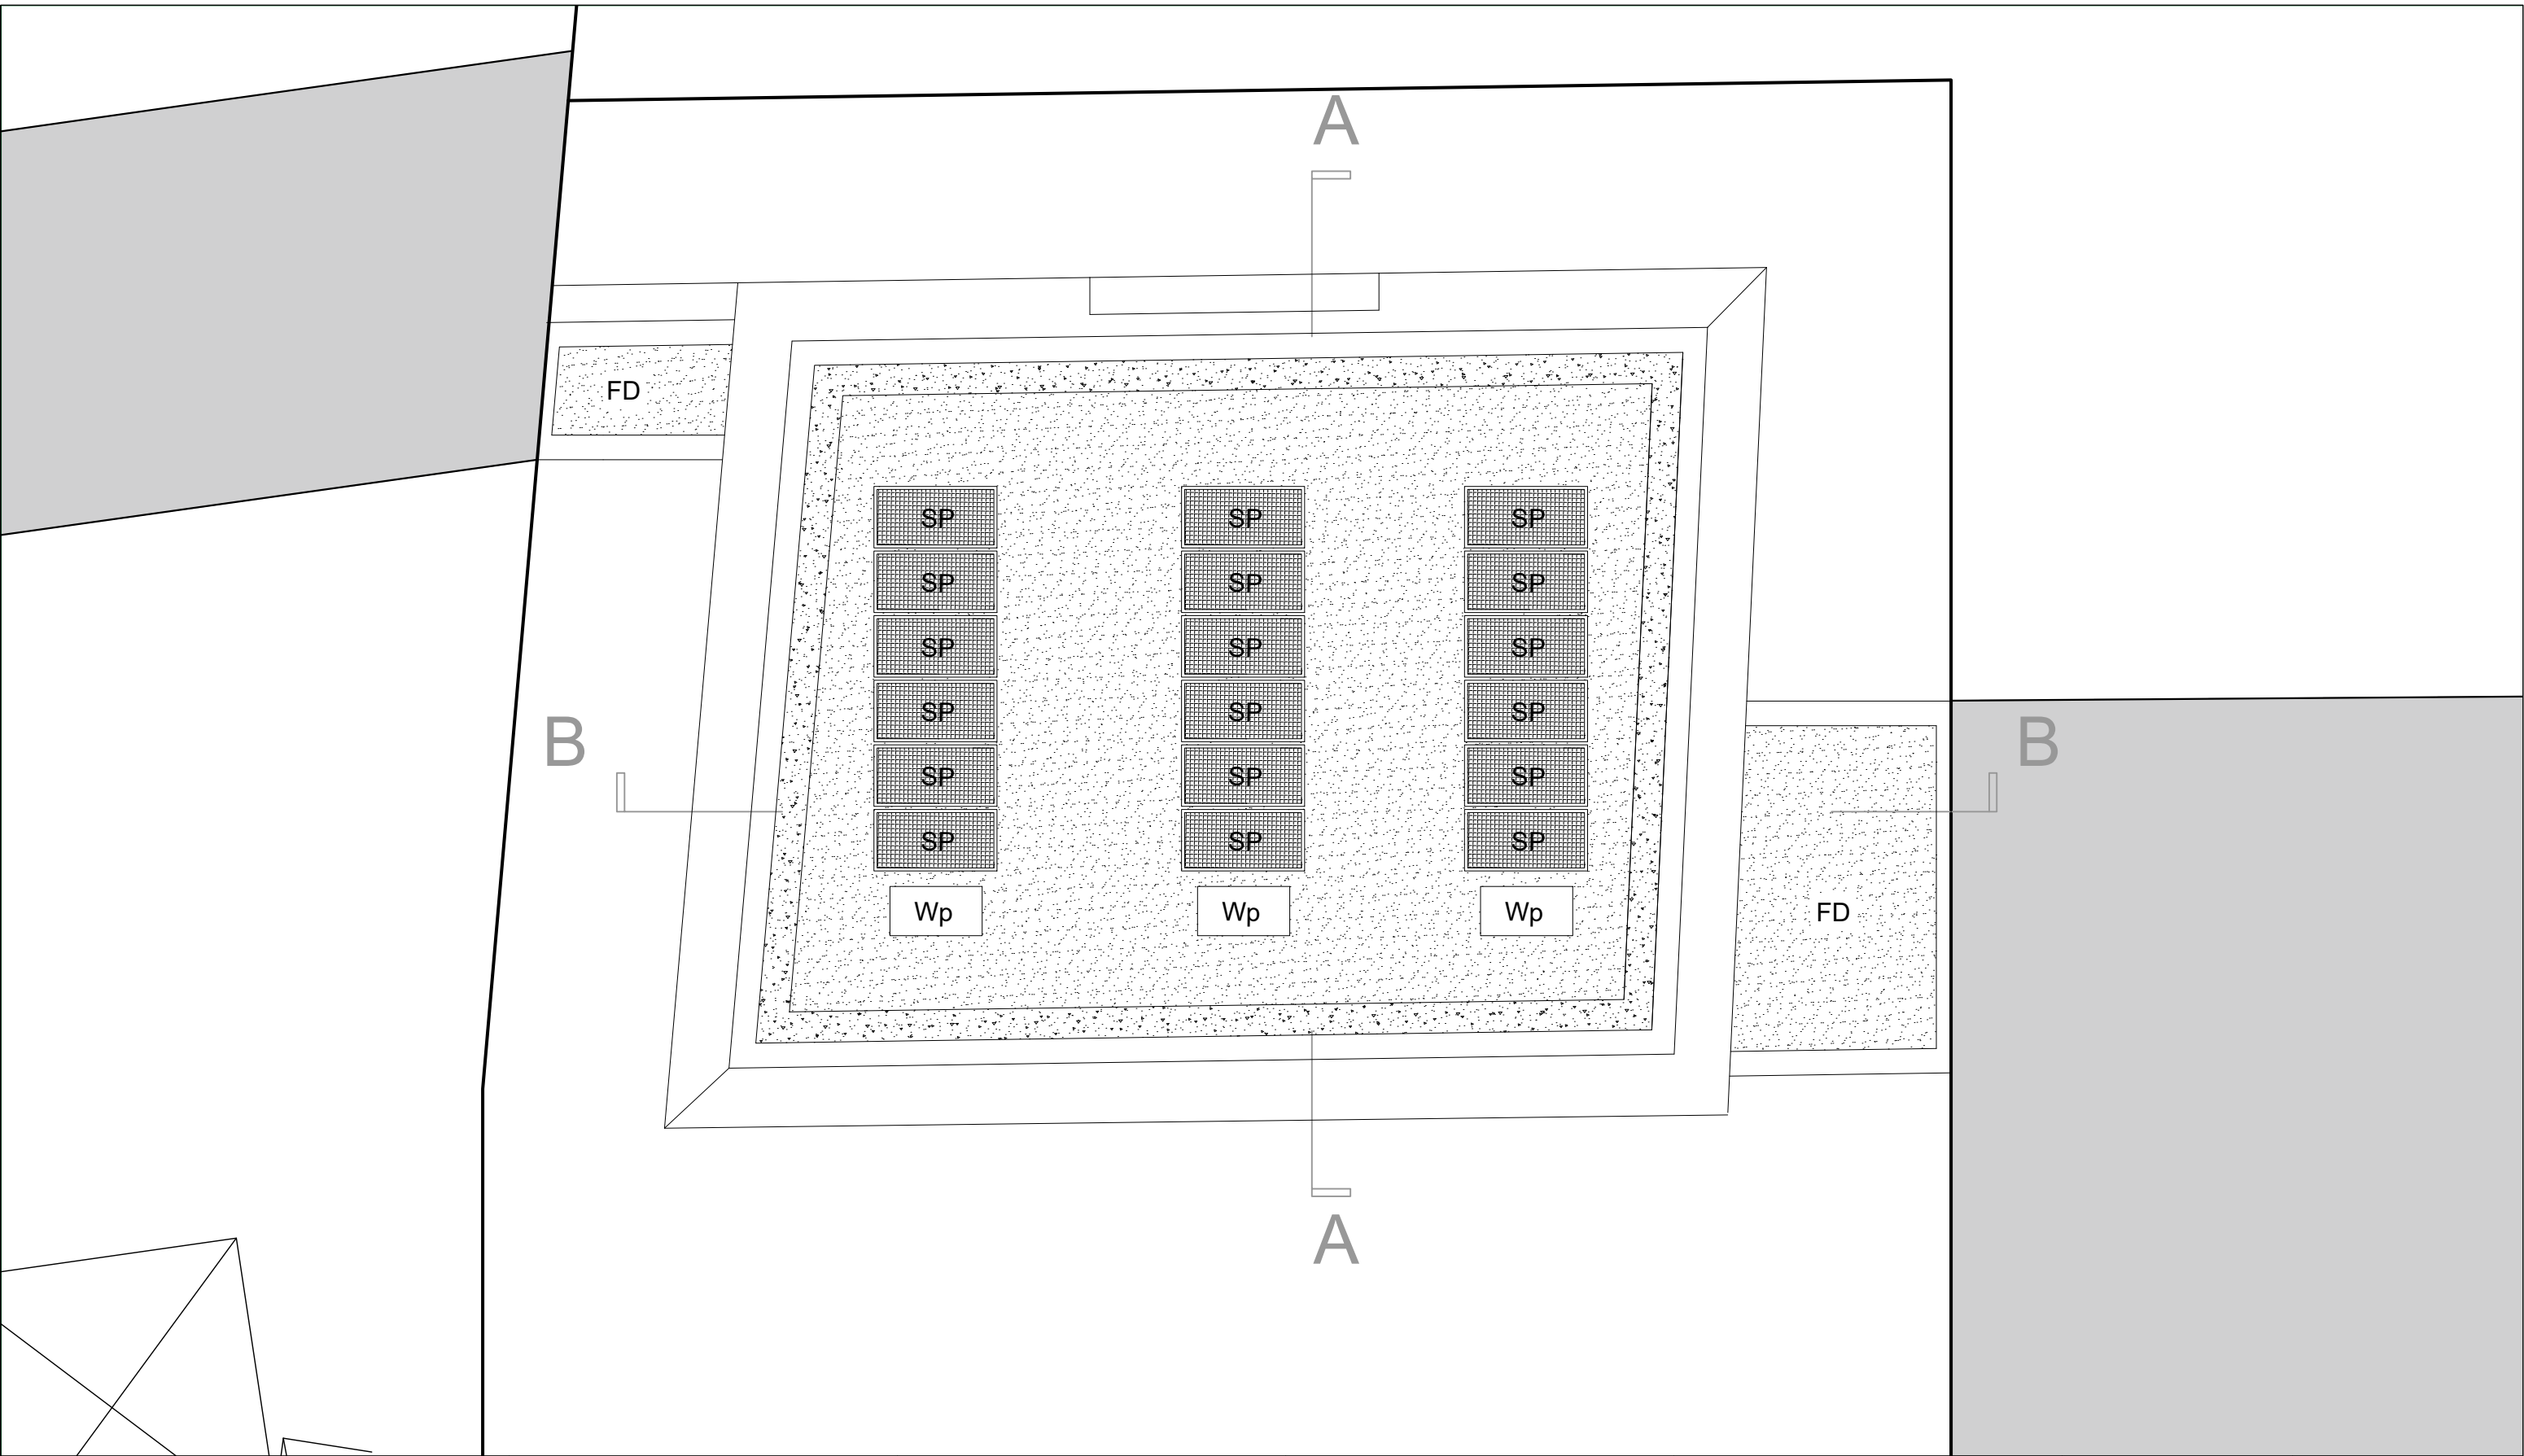


± 0.00 m (± 0.00 = + 35.21m ü DHHN2016) Schnittebene auf 1.0 m über Oberkante Fußboden. Alle Flächen- und Umfangsberechnungen beziehen sich auf Rohbaumaße. Brüstungshöhen sind von OKFF bis OK Rohrüstung angegeben. Höhen von Unter-/ Überzügen verstehen sich incl. Deckenstärke, wenn nicht anders angegeben. PLAN NICHT ZUM BAU FREIGEgeben	Adresse Bauvorhaben	Adresse Bauherr	Unterschrift Bauherr	Unterschrift und Stempel Architekt	S21	Townhouses - Dachaufsicht	
	Schlesische Str. 21 10997 Berlin	GbR Schlesische Str. 21 Moshe Kline Schlesische Str. 21 10997 Berlin			Bauvoranfrage		
					M 1:100	DIN A3	20.12.2024
					architactics Jörn Nolte 10115 Berlin ESSENZ Architecture Cai und Gärtner GbR Esmarchstraße 3 10407 Berlin		

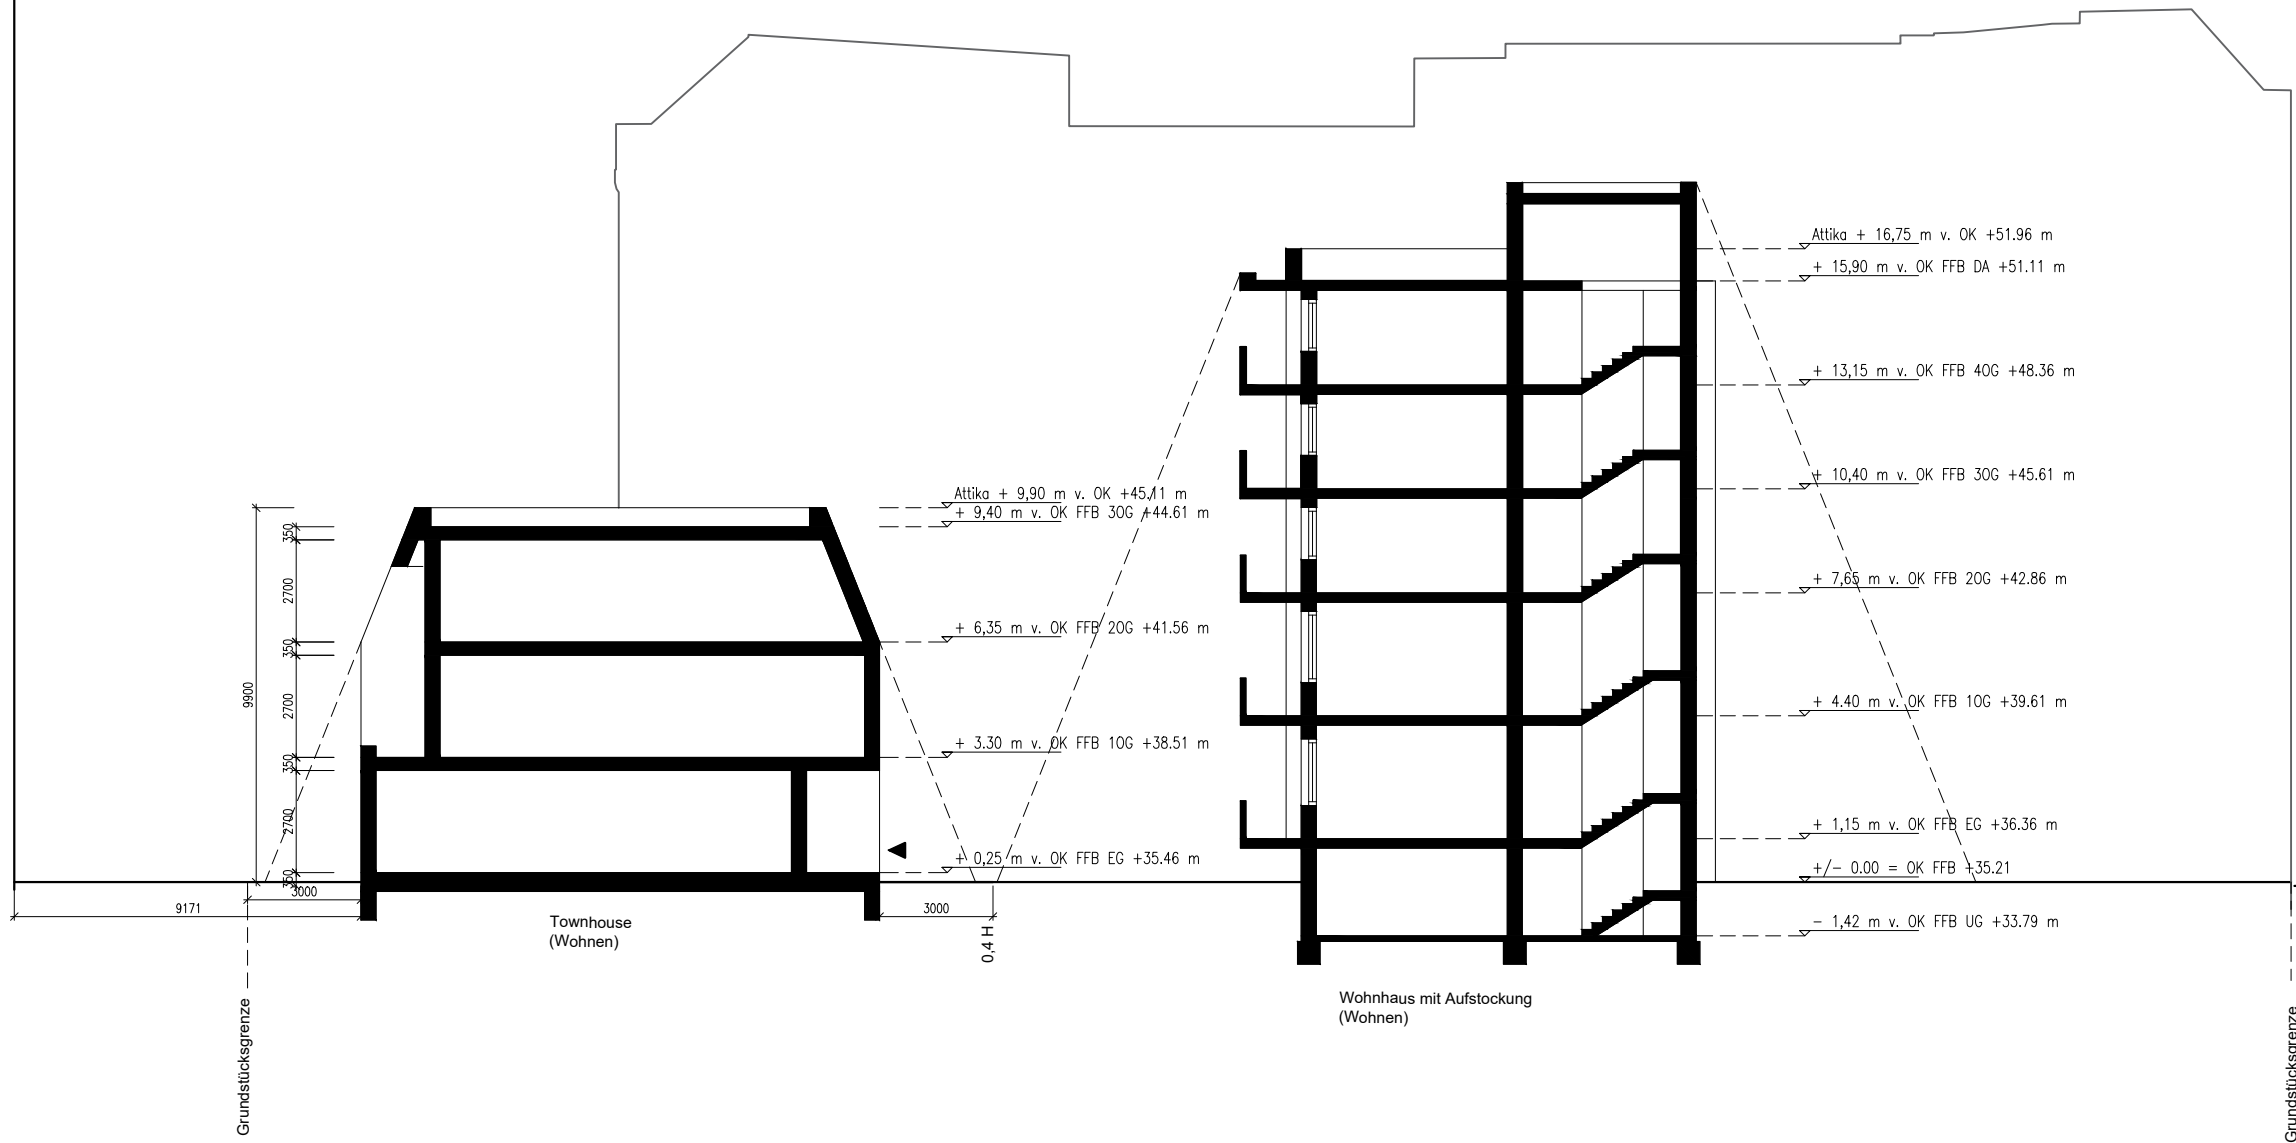


Schnitt A - A

± 0,00 m (± 0,00 = + 35.21m ü DHHN2016) Schnittebene auf 1,0 m über Oberkante Fußboden. Alle Flächen- und Umfangsberechnungen beziehen sich auf Rohbaumaße. Brüstungshöhen sind von OKFF bis OK Rohrüstung angegeben. Höhen von Unter-/ Überzügen verstehen sich incl. Deckenstärke, wenn nicht anders angegeben.	Adresse Bauvorhaben		Adresse Bauherr		Unterschrift Bauherr		Unterschrift und Stempel Architekt		S21		Townhouses - Schnitt A - A	
	Schlesische Str. 21 10997 Berlin		GbR Schlesische Str. 21 Moshe Kline Schlesische Str. 21 10997 Berlin						Bauvoranfrage			
	PLAN NICHT ZUM BAU FREIGEgeben								M 1:200		DIN A3	20.12.2024
									architactics Jörn Nolte 10115 Berlin ESSENZ Architecture Cai und Gärtner GbR Esmarchstraße 3 10407 Berlin			

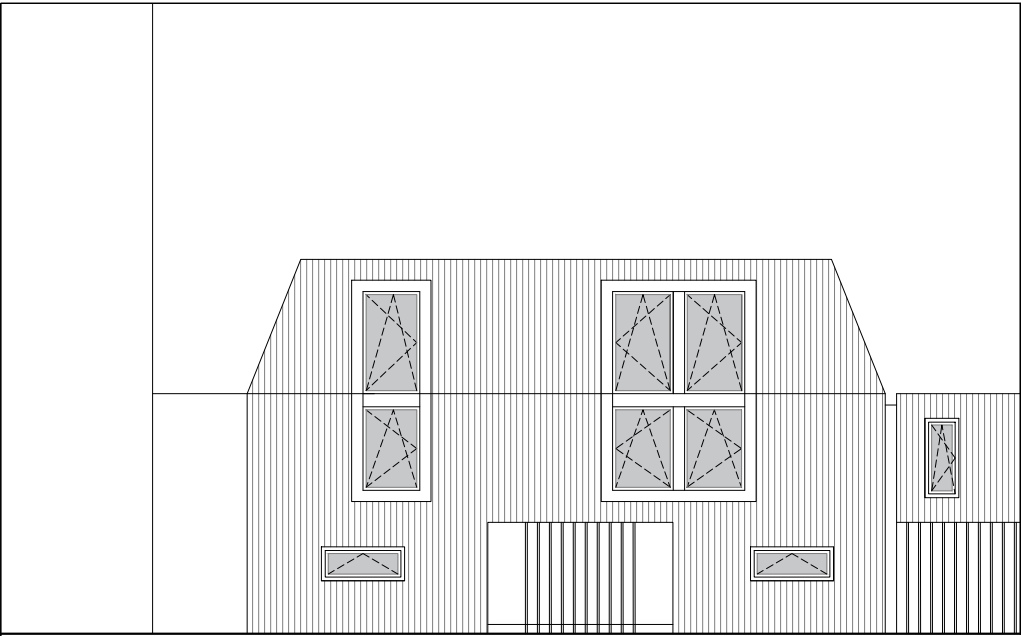

Ansicht von Nordosten

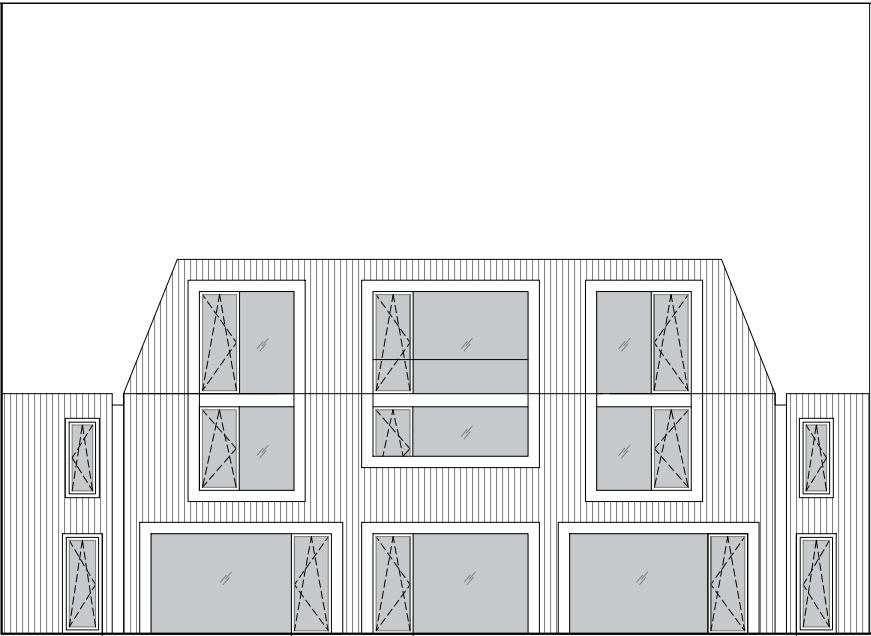


Ansicht von Südwesten

Attika + 9,90 m v. OK +45.11 m
+ 9,40 m v. OK FFB 30G +44.61 m

+ 6,35 m v. OK FFB 20G +41.56 m

+ 3,30 m v. OK FFB 10G +38.51 m

+ 0,25 m v. OK FFB EG +35.46 m

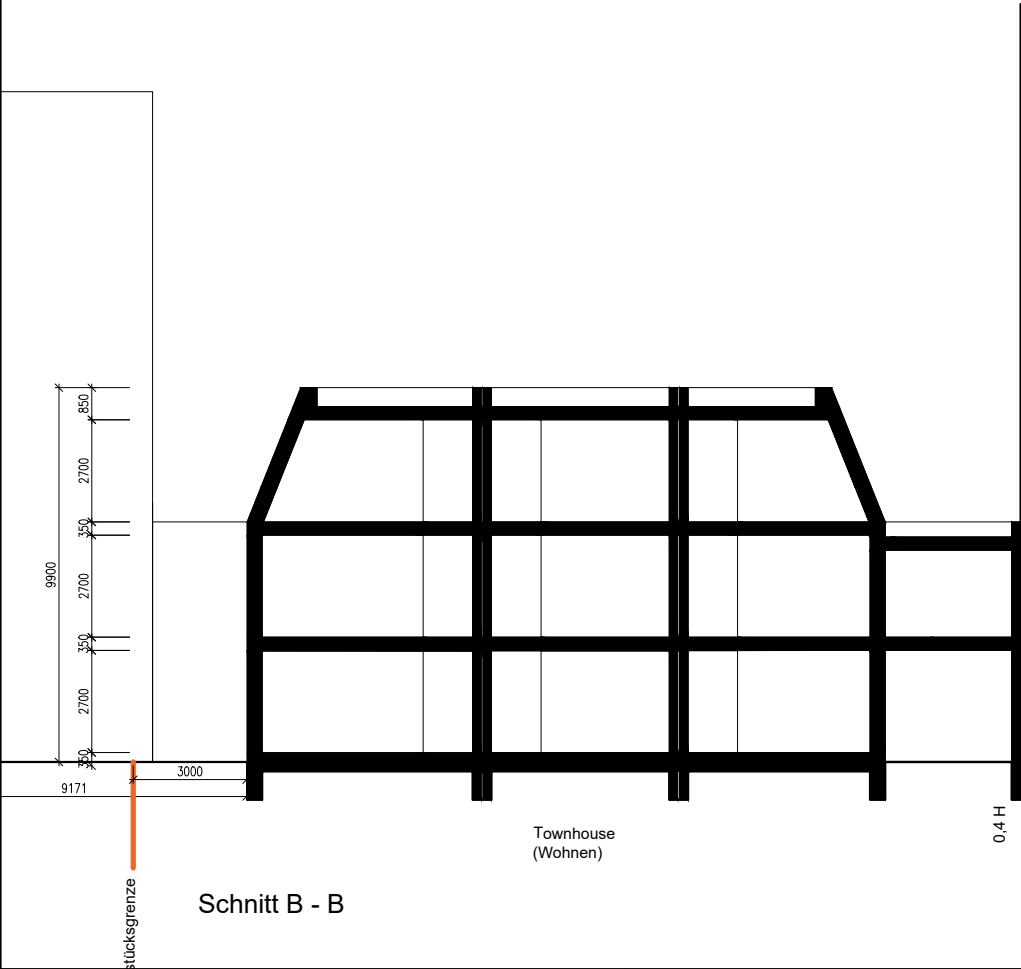


Schnitt B - B

Attika + 9,90 m v. OK +45.11 m
+ 9,40 m v. OK FFB 30G +44.61 m

+ 6,35 m v. OK FFB 20G +41.56 m

+ 3,30 m v. OK FFB 10G +38.51 m

+ 0,25 m v. OK FFB EG +35.46 m

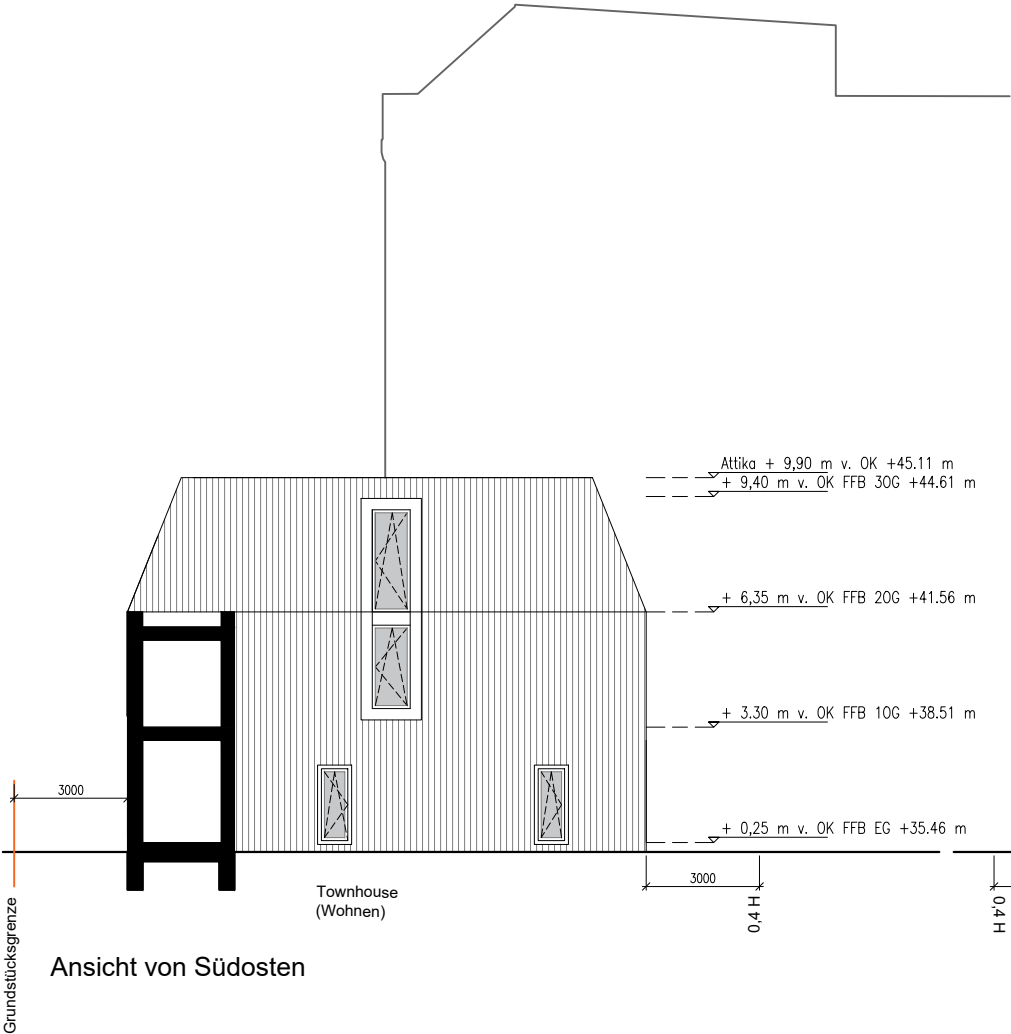


Ansicht von Südosten

Attika + 9,90 m v. OK +45.11 m
+ 9,40 m v. OK FFB 30G +44.61 m

+ 6,35 m v. OK FFB 20G +41.56 m

+ 3,30 m v. OK FFB 10G +38.51 m

+ 0,25 m v. OK FFB EG +35.46 m

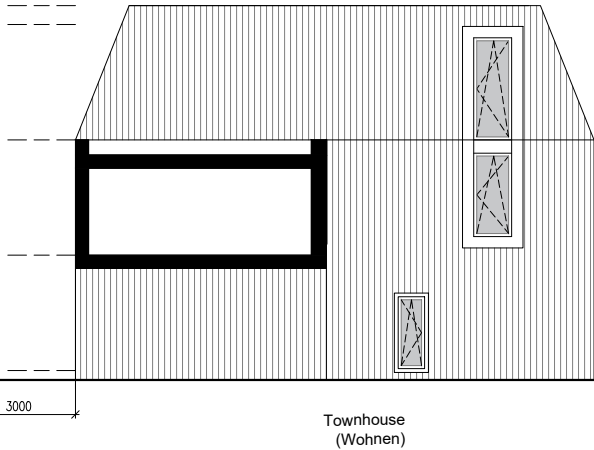

Ansicht von Nordwesten

± 0,00 m (± 0,00 = + 35,21m ü DHHN2016) Schnittebene auf 1,0 m über Oberkante Fußboden. Alle Flächen- und Umfangsberechnungen beziehen sich auf Rohbaumaße. Brüstungshöhen sind von OKFF bis OK Rohrüstung angegeben. Höhen von Unter-/ Überzügen verstehen sich incl. Deckenstärke, wenn nicht anders angegeben. PLAN NICHT ZUM BAU FREIGEgeben	Adresse Bauvorhaben	Adresse Bauherr	Unterschrift Bauherr	Unterschrift und Stempel Architekt	S21	Townhouses - Schnitt B - B, Ansichten	
	Schlesische Str. 21 10997 Berlin	GbR Schlesische Str. 21 Moshe Kline Schlesische Str. 21 10997 Berlin			Bauvoranfrage		
					M 1:200	DIN A3	20.12.2024
					architactics Jörn Nolte 10115 Berlin ESSENZ Architecture Cai und Gärtner GbR Esmarchstraße 3 10407 Berlin		



	Adresse Bauvorhaben	Adresse Bauherr	Unterschrift Bauherr	Unterschrift und Stempel Architekt	<table><tr><td>S21</td><td colspan="2">Perspektive 1</td></tr><tr><td>Bauvoranfrage</td><td colspan="2"></td></tr><tr><td></td><td>DIN A3</td><td>20.12.2024</td></tr></table>			S21	Perspektive 1		Bauvoranfrage				DIN A3	20.12.2024
S21	Perspektive 1															
Bauvoranfrage																
	DIN A3	20.12.2024														
± 0,00 m (± 0,00 = + 35.21m ü DHHN2016) Schnittebene auf 1,0 m über Oberkante Fußboden. Alle Flächen- und Umfangsberechnungen beziehen sich auf Rohbaumaße. Brüstungshöhen sind von OKFF bis OK Rohrbrüstung angegeben. Höhen von Unter-/ Überzügen verstehen sich incl. Deckenstärke, wenn nicht anders angegeben.	Schlesische Str. 21 10997 Berlin	GbR Schlesische Str. 21 Moshe Kline Schlesische Str. 21 10997 Berlin			architactics Jörn Nolte 10115 Berlin ESSENZ Architecture Cai und Gärtner GbR Esmarchstraße 3 10407 Berlin											
PLAN NICHT ZUM BAU FREIGEgeben																



± 0,00 m (± 0,00 = + 35,21m ü DHHN2016) Schnittebene auf 1,0 m über Oberkante Fußboden. Alle Flächen- und Umfangsberechnungen beziehen sich auf Rohbaumaße. Brüstungshöhen sind von OKFF bis OK Rohbrüstung angegeben. Höhen von Unter-/ Überzügen verstehen sich incl. Deckenstärke, wenn nicht anders angegeben.	Adresse Bauvorhaben Schlesische Str. 21 10997 Berlin	Adresse Bauherr GbR Schlesische Str. 21 Moshe Kline Schlesische Str. 21 10997 Berlin	Unterschrift Bauherr		S21		Perspektive 2	
					Bauvoranfrage			
						DIN A3	20.12.2024	
					architactics Jörn Nolte 10115 Berlin ESSENZ Architecture Cai und Gärtner GbR Esmarchstraße 3 10407 Berlin			
PLAN NICHT ZUM BAU FREIGEgeben								



± 0,00 m (± 0,00 = + 35,21m ü DHHN2016) Schnittebene auf 1,0 m über Oberkante Fußboden. Alle Flächen- und Umfangsberechnungen beziehen sich auf Rohbaumaße. Brüstungshöhen sind von OKFF bis OK Rohbrüstung angegeben. Höhen von Unter-/Überzügen verstehen sich incl. Deckenstärke, wenn nicht anders angegeben.	Adresse Bauvorhaben		Adresse Bauherr		Unterschrift Bauherr		Unterschrift und Stempel Architekt		S21	Perspektive 3	
	Schlesische Str. 21 10997 Berlin		GbR Schlesische Str. 21 Moshe Kline Schlesische Str. 21 10997 Berlin						Bauvoranfrage		
										DIN A3	20.12.2024
	PLAN NICHT ZUM BAU FREIGEgeben								architactics Jörn Nolte 10115 Berlin ESSENZ Architecture Cai und Gärtner GbR Esmarchstraße 3 10407 Berlin		

