


30 | 3.88 | 5.36⁵ | 3.51 | 2.67⁵ | 3.51 | 30 | 4.01 | 30 | 2
 30 | 3.95 | 24 | 2.59⁵ 9⁵ | 2.07⁵ 9⁵ | 3.77⁵ 24 | 2.07⁵ 9⁵ | 3.71⁵ 24 | 4.06 | 30 | 2

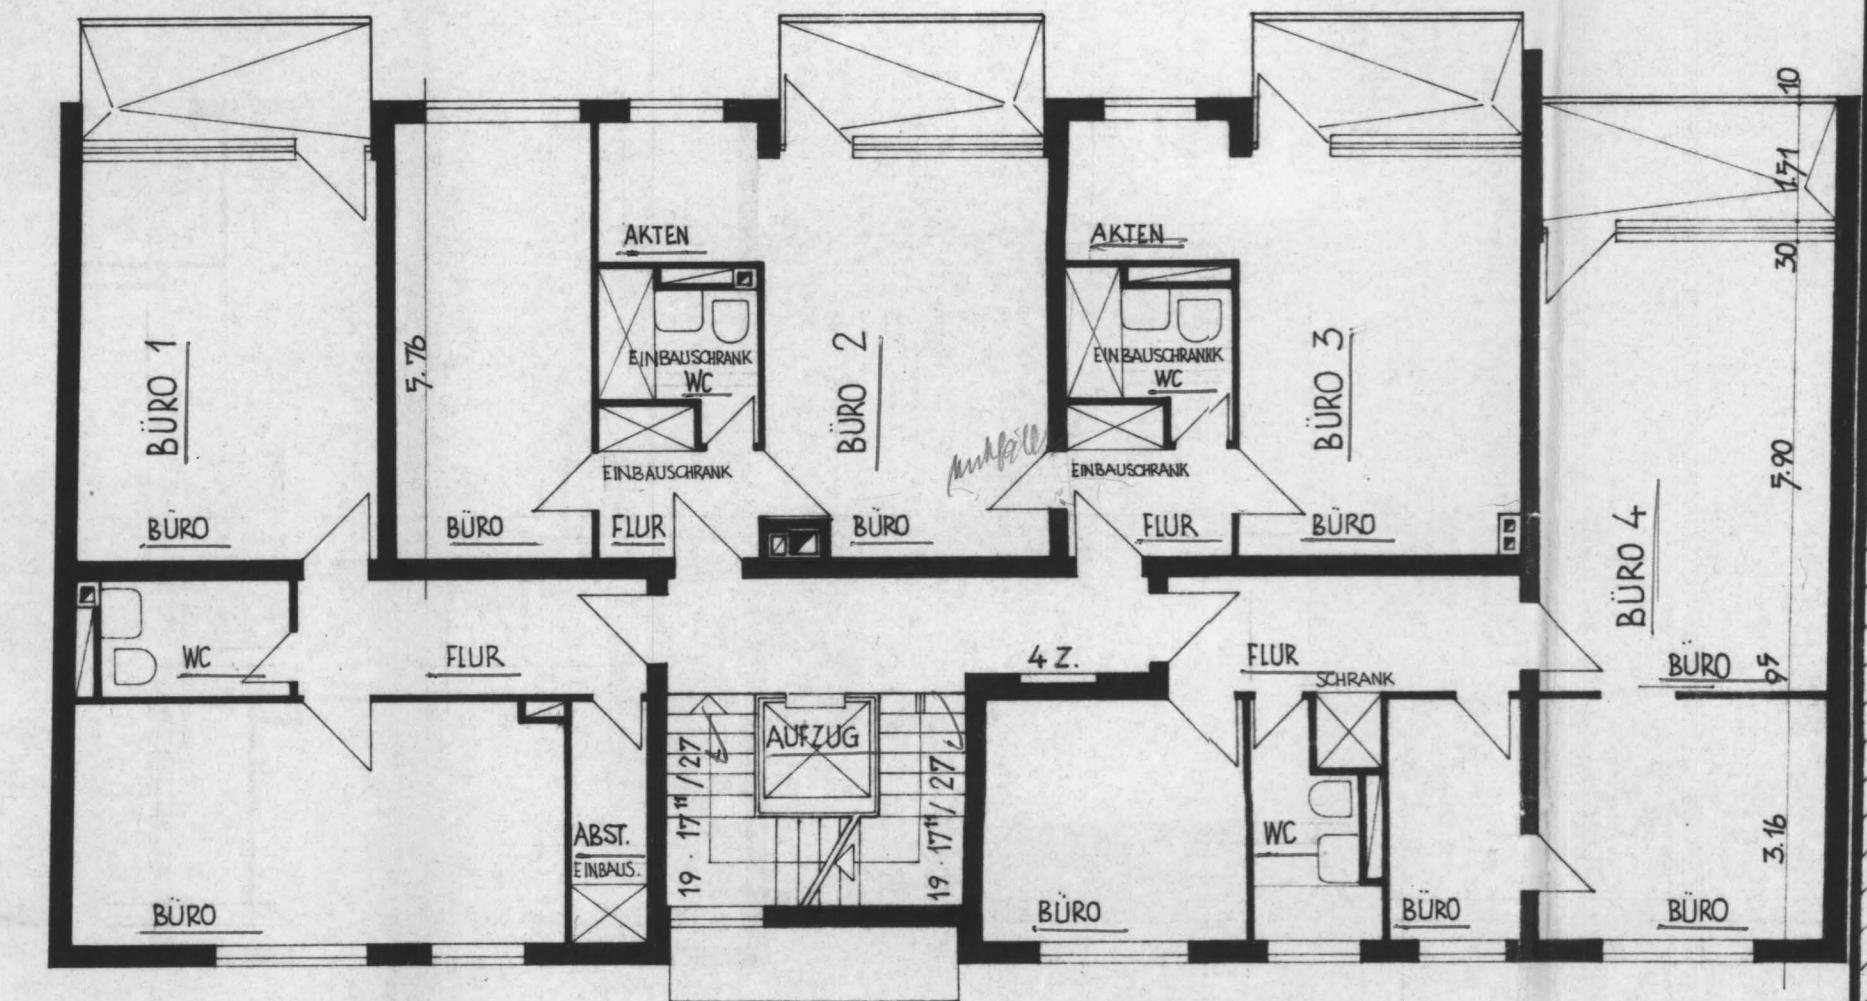


GEWERBETEIL

30 | 6.60⁵ 9⁵ | 100 | 30 | 30 | 3.37 9⁵ | 1.70 9⁵ | 1.80 | 24 | 3.76 | 30 | 2
 8.30 | 3.89 | 11.66 | 23.85

1. OBERGESCHOSS


30 | 3.88 | 5.36⁵ | 3.51 | 2.67⁵ | 3.51 | 30 | 4.01 | 30 | 2
 30 | 3.95 | 24 | 2.59⁵ 9⁵ | 2.07⁵ 9⁵ | 3.77⁵ 24 | 2.07⁵ 9⁵ | 3.71⁵ 24 | 4.06 | 30 | 2

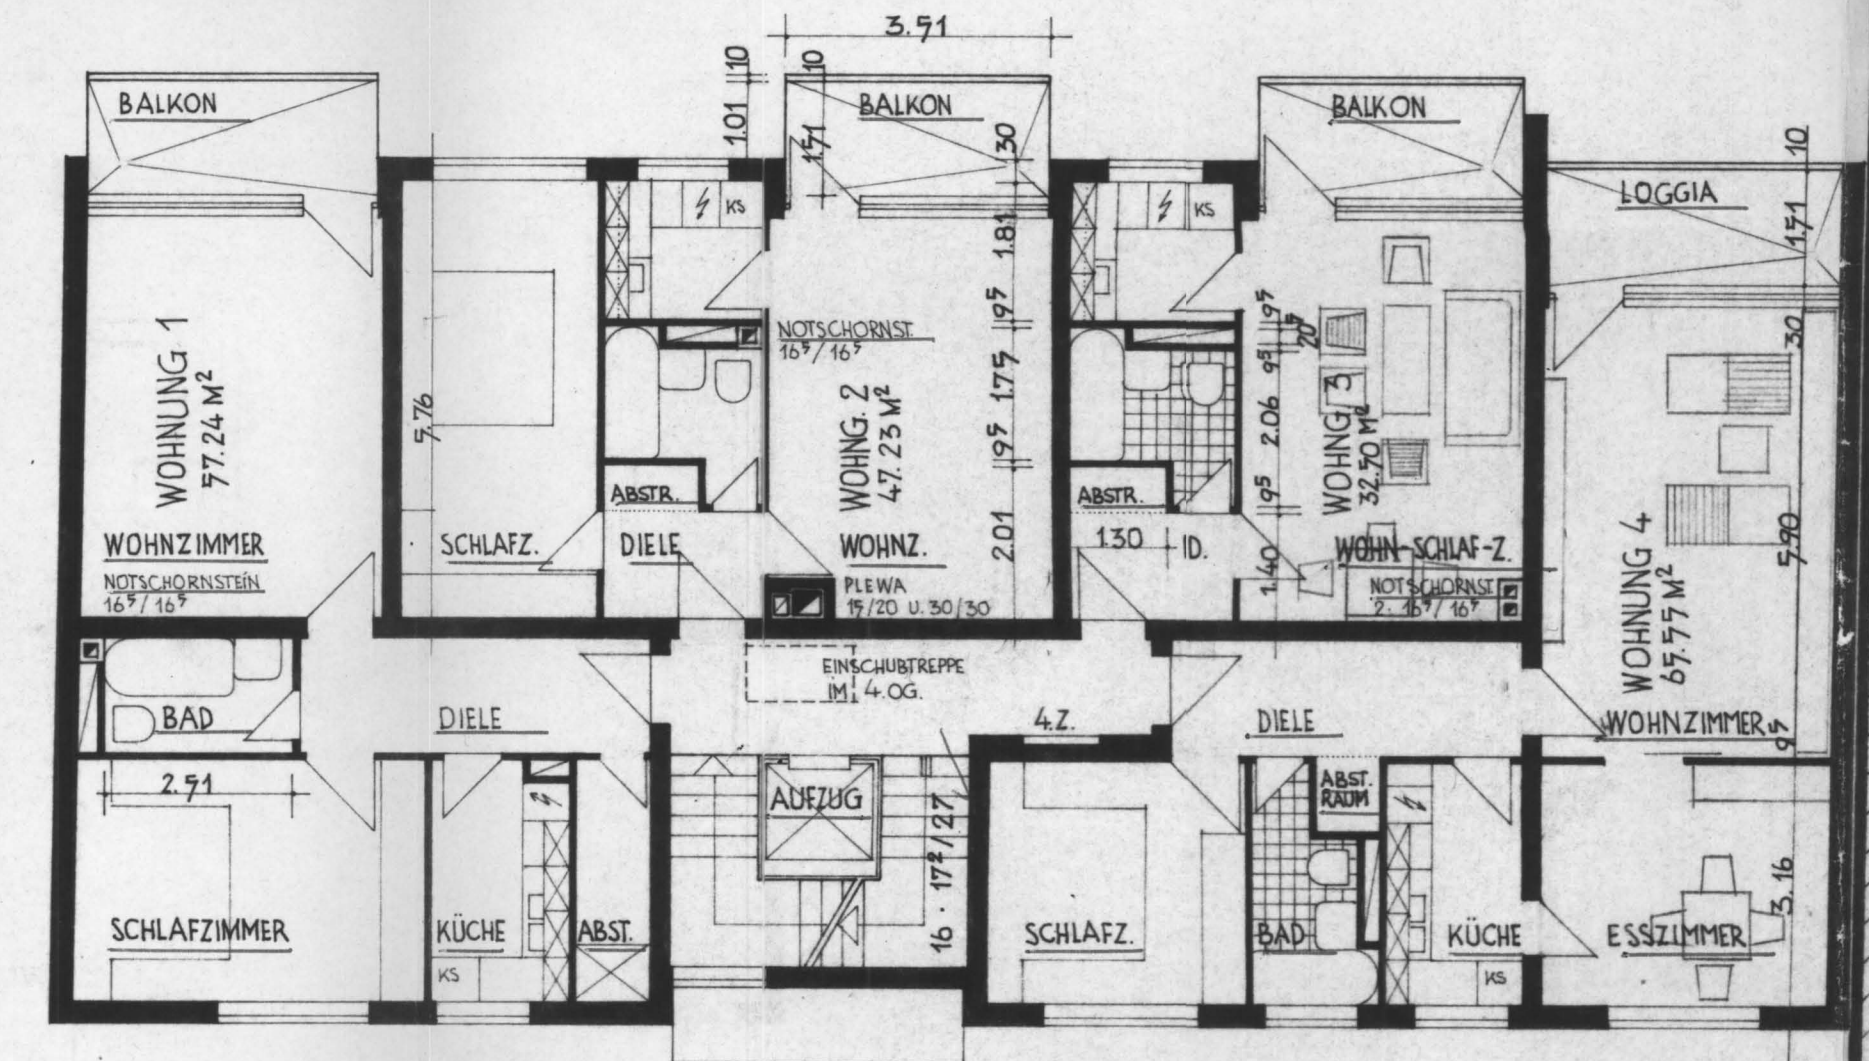

WOHNTEIL

30 | 4.71 9⁵ | 1.80 9⁵ | 100 | 30 | 30 | 3.37 9⁵ | 1.70 9⁵ | 1.80 | 24 | 3.76 | 30 | 2
 2.24 | 2.01 1.38⁵ | 86⁵ 1.26 76 | 1.92⁵ 1.26 2.51 | 2.63 1.06 | 2.01 1.38⁵ | 86⁵ 1.26 76 | 1.26 1.24 | 2.01 1.38⁵ | 1.21⁵
 8.30 | 3.89 | 11.66 | 23.85

2. OBERGESCHOSS

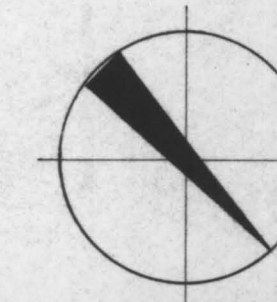

BLATT NR. 3

BAUVORHABEN:
 1 BERLIN 36
 SCHLESISCHE STR. 21

1.-4. OBERGESCHOSS

M 1:100

Gehört zum Befreiungsentscheid vom
 als Nachtrag Nr. 340 vom 8.3.68
 zur Baugenehmigung Nr. 340 vom 8.3.68
 zur Reklamation Nr. vom
 Geprüft
 hinsichtlich der farbigen Eintragungen
 Berlin, den 24. Februar 1968
 Bauplanungsamt
 Abt. Bau- und Wohnungswesen
 - Bauleitung
 im Auftrag

BAUHERR:

Heinz Mosch
 Elektrohandel KG

PLANUNG:

Geschäfts- und Wohnbauten
 Heinz Mosch
 Gesellschaft m.b.H. & Co. KG

BERLIN, 29. JAN. 1968

GEL: Matema MAT