


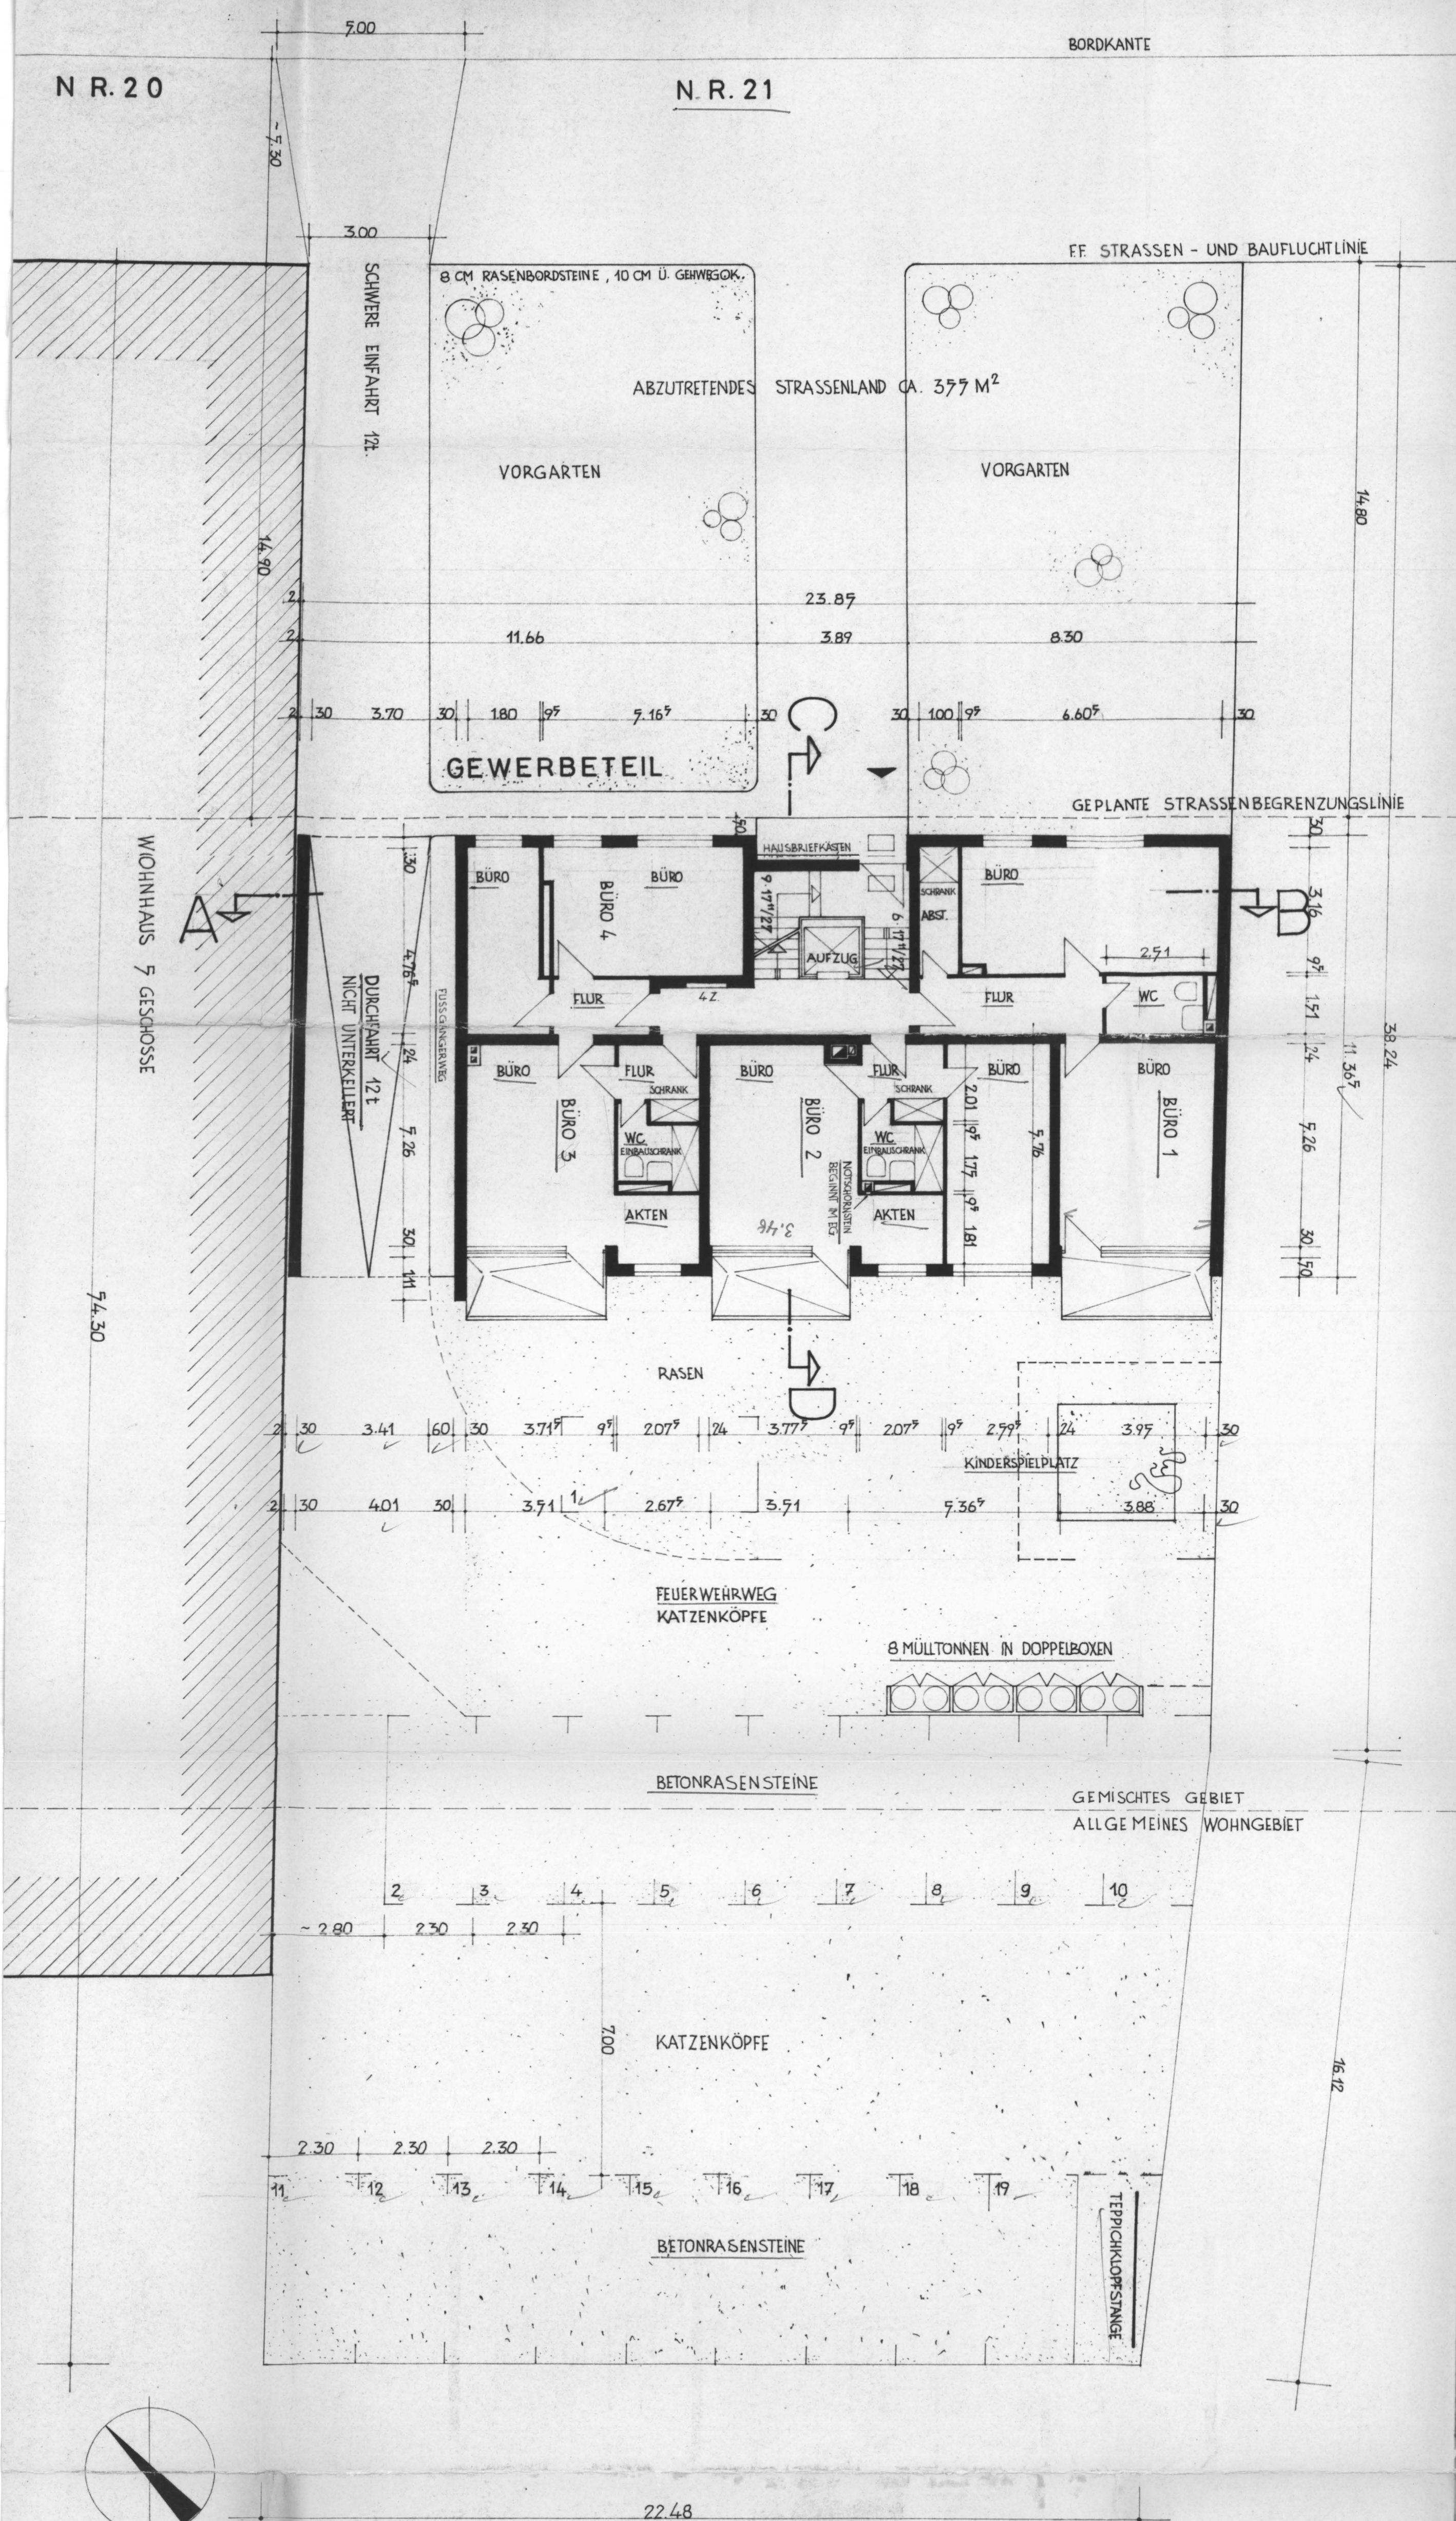

als Gekauft zum Aufgangesteichfeld vom _____
 die Forderung Nr. 340 vom 8.3.1968
 zur Rangabgleichung Nr. _____
 zur Rangabgleichung Nr. _____ vom _____

Geprüft

hinsichtlich der farbigen Eintragungen
 Berlin, den 21. Februar 1968
 Bezirksamt Kreuzberg von Berlin
 Abt. Bau- und Wohnungswesen

Gepüft

BAUHER:

Heinz Mosch
Elektrohandel KG

PLANUNG:

Geschäfts- und Wohnbauten

Heinz Mosch

Gesellschaft m.b.H. & Co. KG

BERLIN JAN. 1968

GEZ: *Materna* MAT.

BLATT NR. 2

BAUVORHABEN:
1 B E R L I N 36
SCHLESISCHE STR. 21

ERDGESCHOSS
M 1:100

M 1:100

BAUHER:

Heinz Mosch
Elektrohandel KG

PLANUNG:

Geschäfts- und Wohnbauten

Heinz Mosch

Gesellschaft m.b.H. & Co. KG

BERLIN JAN. 1968

GEZ: *Materna* MAT.