


30 | 3.88 | 7.36⁷ | 3.51 | 2.67⁷ | 3.51 | 30 | 4.31 | 2
 30 | 2.99⁷ | 24 | 1.93 | 30 | 30 | 2.07⁷ | 30

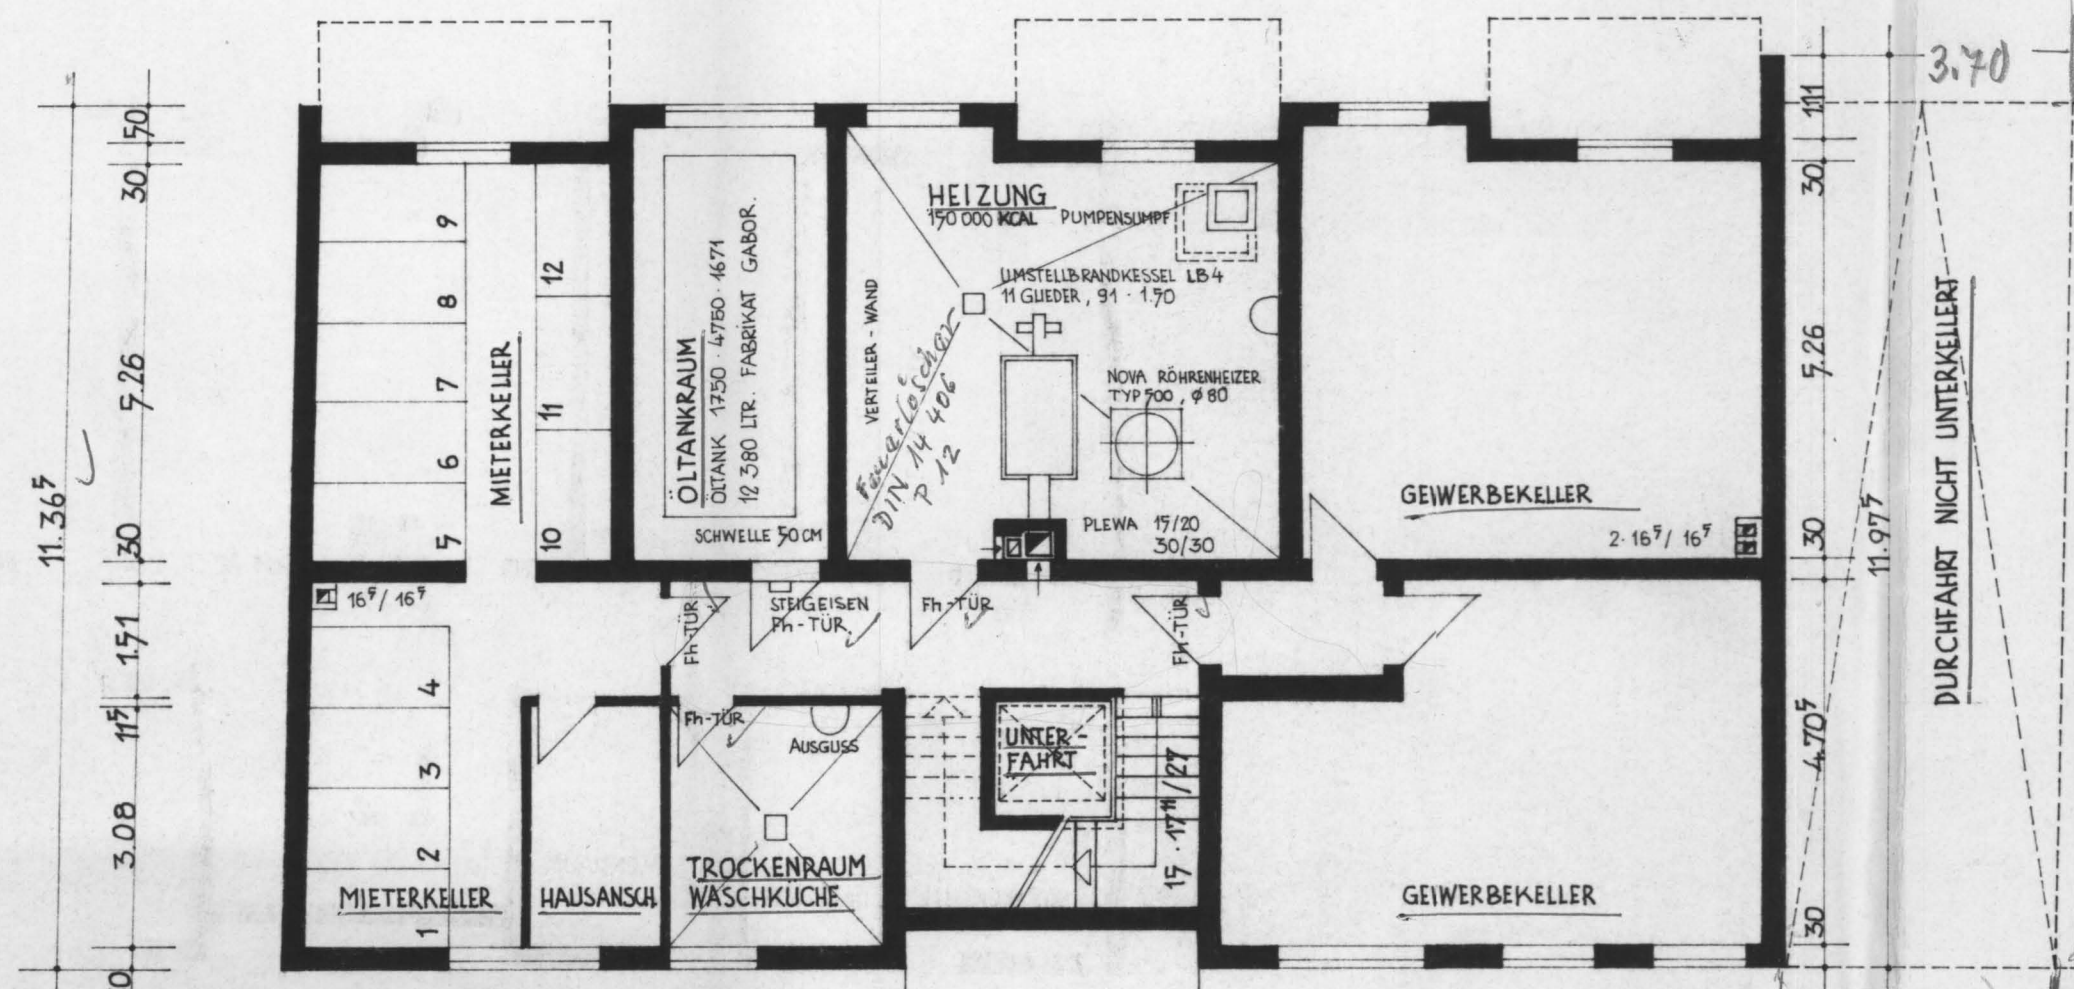


30 | 2.88⁷ | 11⁵ | 170 | 11⁵ | 2.88⁷ | 30 | 7.06 | 30 | 3.65
 8.30 | 3.89 | 7.66 | 4.00 | 2
 23.87

KELLERGEOSCH


4.18 | 7.36⁷ | 3.51 | 2.67⁷ | 3.81 | 4.31
 24 | 3.70 | 24 | 24 | 3.03 | 24 | 24 | 3.33 | 24 | 4.07 | 24 | 2

12.47⁷
 11.99⁷
 24

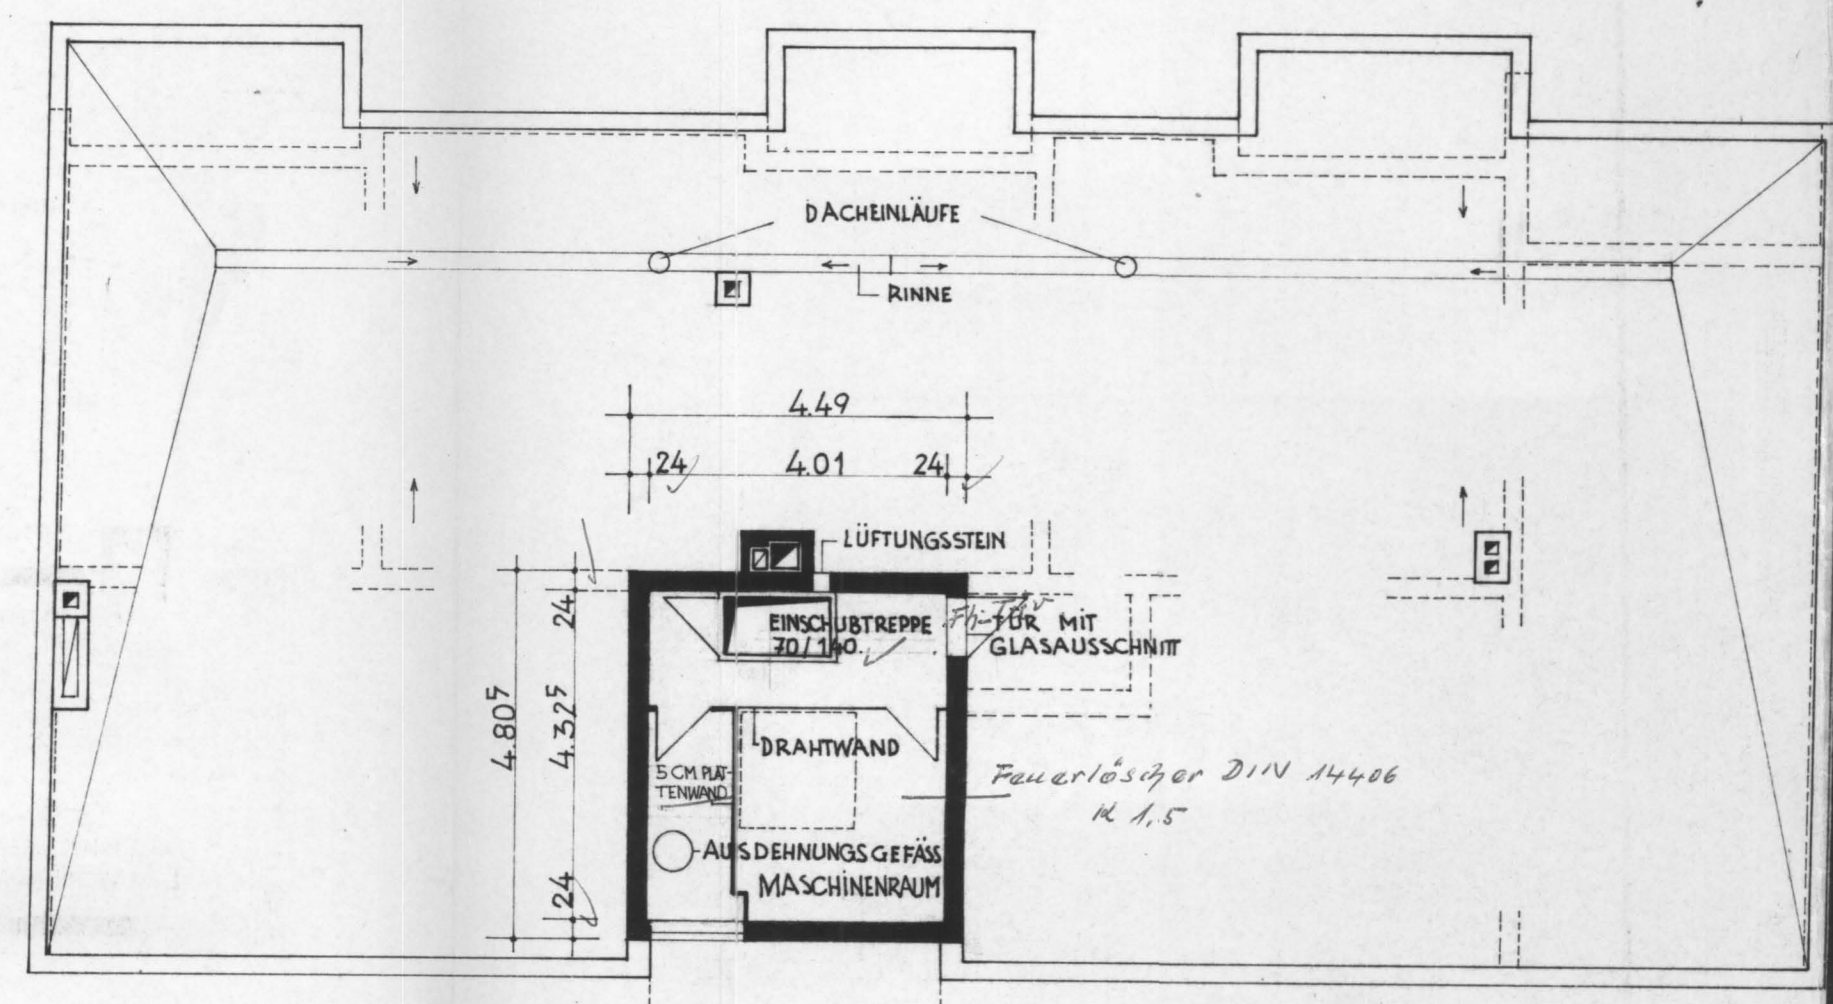

24 | 7.76 | 30 | 30 | 11.12 | 24
 8.30 | 3.89 | 11.66
 23.87

DACHAUF SICH T

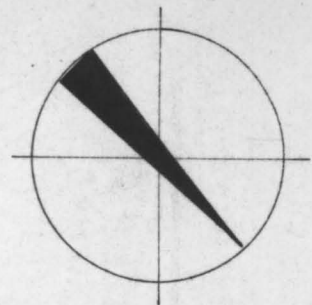

Pol. Neumann
 Fa. Mosch

BLATT NR. 1

BAUVORHABEN:
 1 BERLIN 36
 SCHLESISCHE STR. 21

KELLER U. DACHAUF S.
 M 1:100

BAUHERR:

Heinz Mosch
 Elektrohandel KG

PLANUNG:

Geschäfts- und Wohnbauten
 Heinz Mosch
 Gesellschaft m.b.H. & Co. KG

BERLIN, 29. JAN. 1968
 GEZ. Matern

Gehört zum Befreiungsentscheid vom
 als Nachtrag Nr. 340 vom 8.3.68
 zur Baugenehmigung Nr. vom
 zur Reklamationen-Nr. vom
 Geprüft
 hinsichtlich der farbigen Eintragungen
 Berlin, den 21. Februar 1968
 Bes. Amt Krenzberg von Berlin
 Abt. Bau- und Wohnungswesen
 - Bauaufsichtsamt -
 Im Auftrage
 Krenzberg