


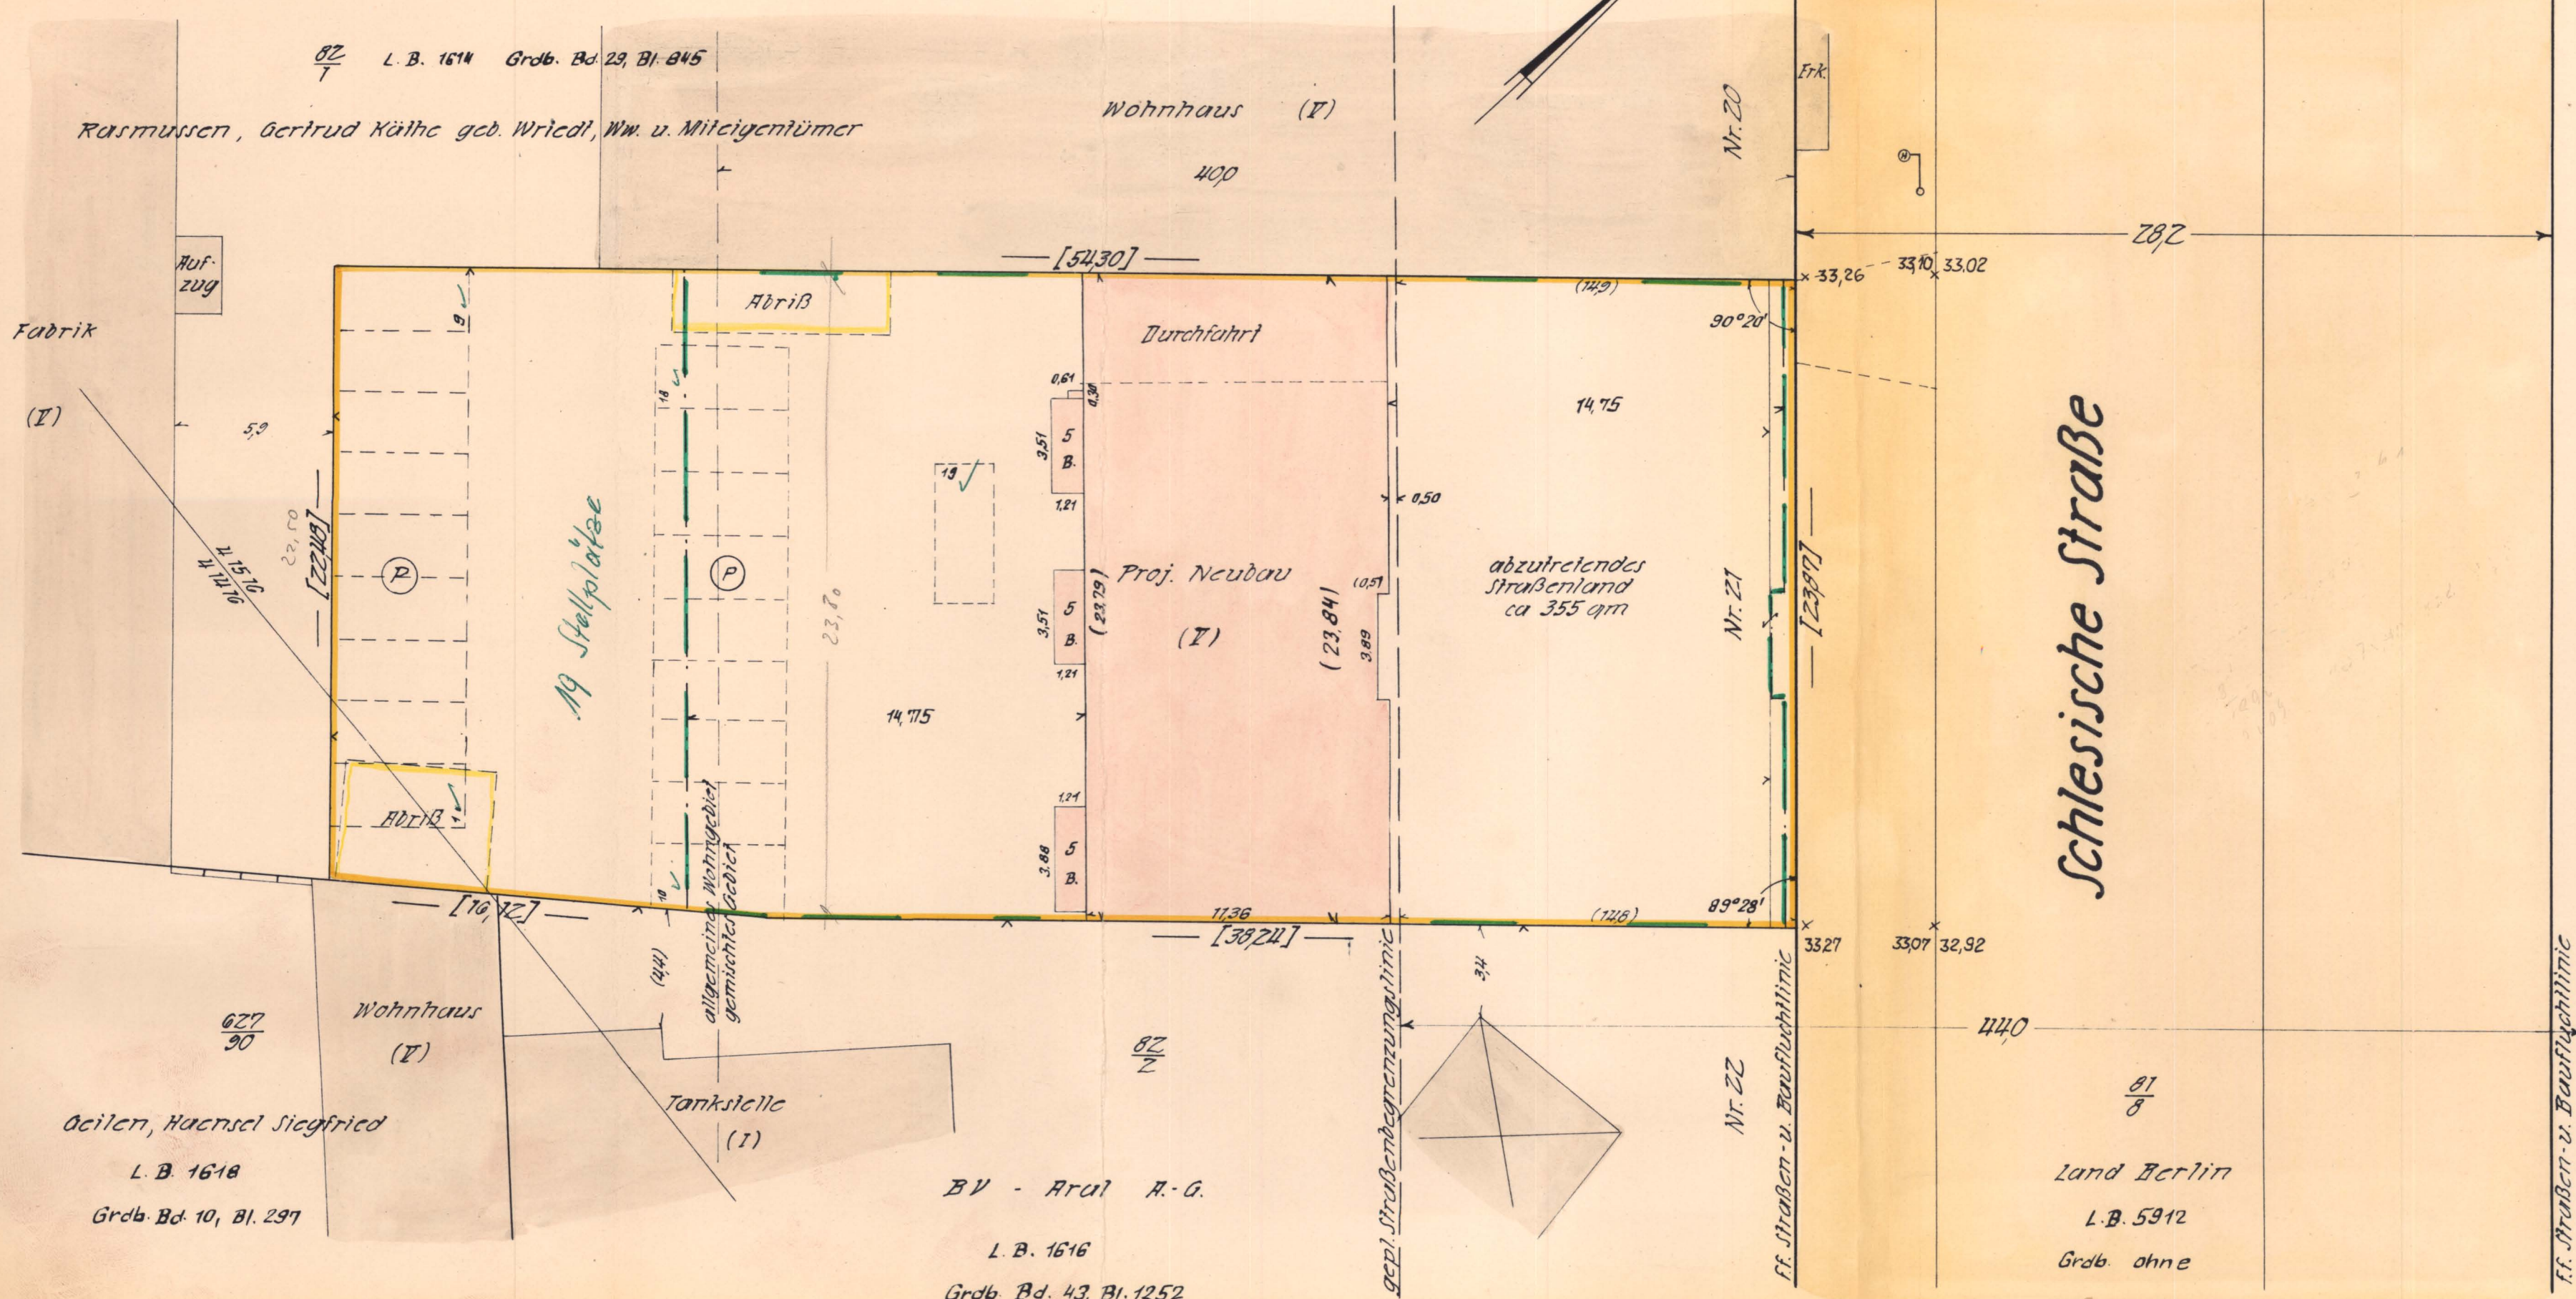

82
L. B. 1614 Grdb. Bd. 29, Bl. 845
Rasmussen, Gertrud Käthe geb. Wriedt, Wm. u. Miteigenümer

627
90
Oelen, Haensel Siegfried
L. B. 1618
Grdb. Bd. 10, Bl. 297

BV - Aral A.G.
L. B. 1616
Grdb. Bd. 43, Bl. 1252

Land Berlin
L. B. 5912
Grdb. ohne

Höhen ü. N.N.

Geklammerte Maße sind graphisch ermittelt

Flächennachweis
Grundstückgröße lt. Kataster und Bauplan 1287 qm
Zul. Bebauung (Bauz. 113) 1287 qm
Proj. Neubau 386,70 qm
 $\frac{1}{2}(23,84 + 23,79) \cdot 11,36 = 270,54$
 $0,5 \cdot 3,89 = 1,94$
 $0,61 \cdot 0,30 = 0,18$
 $2 \cdot 3,51 \cdot 1,21 \cdot \frac{1}{2} = 4,25$
 $3,88 \cdot 1,21 \cdot \frac{1}{2} = 2,35$
275,38 qm
110,72 qm
1376,90 qm
1376,90 qm


Noch bebaubar: 110,72 qm
Geschoßflächenzahl 1376,90 : 1287 = 1,07
Geschoßflächenzahl nach gepl. Fluchtlinien 1376,90 : 932 = 1,48 (Zul. 1.5)

Gebört zum Befreiungsscheid vom
als Nachtrag Nr. 340 vom 8.3.68
zur Baugenehmigung Nr. 340 vom 8.3.68
zur Reklamegenehm. Nr. vom

Grenzbescheinigung erforderlich.
(gem. Rd. Verf. Senator Bau/Wohn Nr. 50/58 vom 24.9.1956)
Öffentl. bestellter Vermessungsingenieur.

Geprüft
hinsichtlich der fachl. Eintragungen
Berlin, den 21. Februar 1968
Bezirksamt Kreuzberg von Berlin
Abt. Bau- und Wohnungswesen
— Bauaufsicht —
im Auftr. Schmalz

Katasternachweis
Gemarkung Berlin, Flur 1
Flurstück 3507182 = 1287 qm
Liegenschaftsbuch Nr. 1615
Grundbuch Bd. 29, Bl. 846 u. 847, Tor
Eigtl.: KG. in Fa. Robert Karst

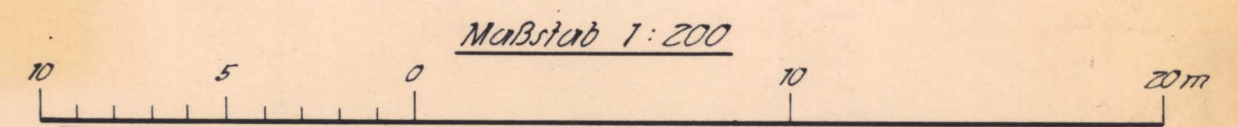

[...], Maße aus Akten des Bauaufsichtsamtes 6/176

Berlin
Bezirk Kreuzberg

Änderungen:
1.2.1968 Projektänd.

Lageplan

von dem Grundstück

Berlin - Kreuzberg

Schlesische Straße 21

Gefertigt nach öff. Aufnahme und amtlichen Unterlagen Berlin 26 (Wittenau) den 3.7.1965 Orlanburger Str. 213 (412.36.21) Die Richtigkeit der Aufnahme wird mit der Öffentlichkeit bescheinigt.



Öffentl. best. Verm.-Ing.
Hufn.-Nr. 248/65