



BLATT NR. 4

BAUVORHABEN:
1 BERLIN 36
SCHLESISCHE STR. 21

133

SCHNITTE A-B, C-D
M 1:100

Gebört zum Befreiungsecheid vom
als Nachtrag Nr. 340 vom 8.3.68
zur Baugenehmigung Nr. 340 vom 8.3.68
zur Reklamegenehm. Nr. vom

Geprüft
hinsichtlich der farbigen Eintragungen
Berlin, den 21. Februar 1968
Bezirksamt Kreuzberg von Berlin
Abt. Bau- und Wohnungswesen
- Bauaufsichtsamt -
Im Auftrag

BAUHERR:


Heinz Mosch
Elektrohandel KG

PLANUNG:


Geschäfts- und Wohnbauten
Heinz Mosch
Gesellschaft m.b.H. & Co. KG

BERLIN, 29. JAN. 1968

GEZ. Matrone MAT

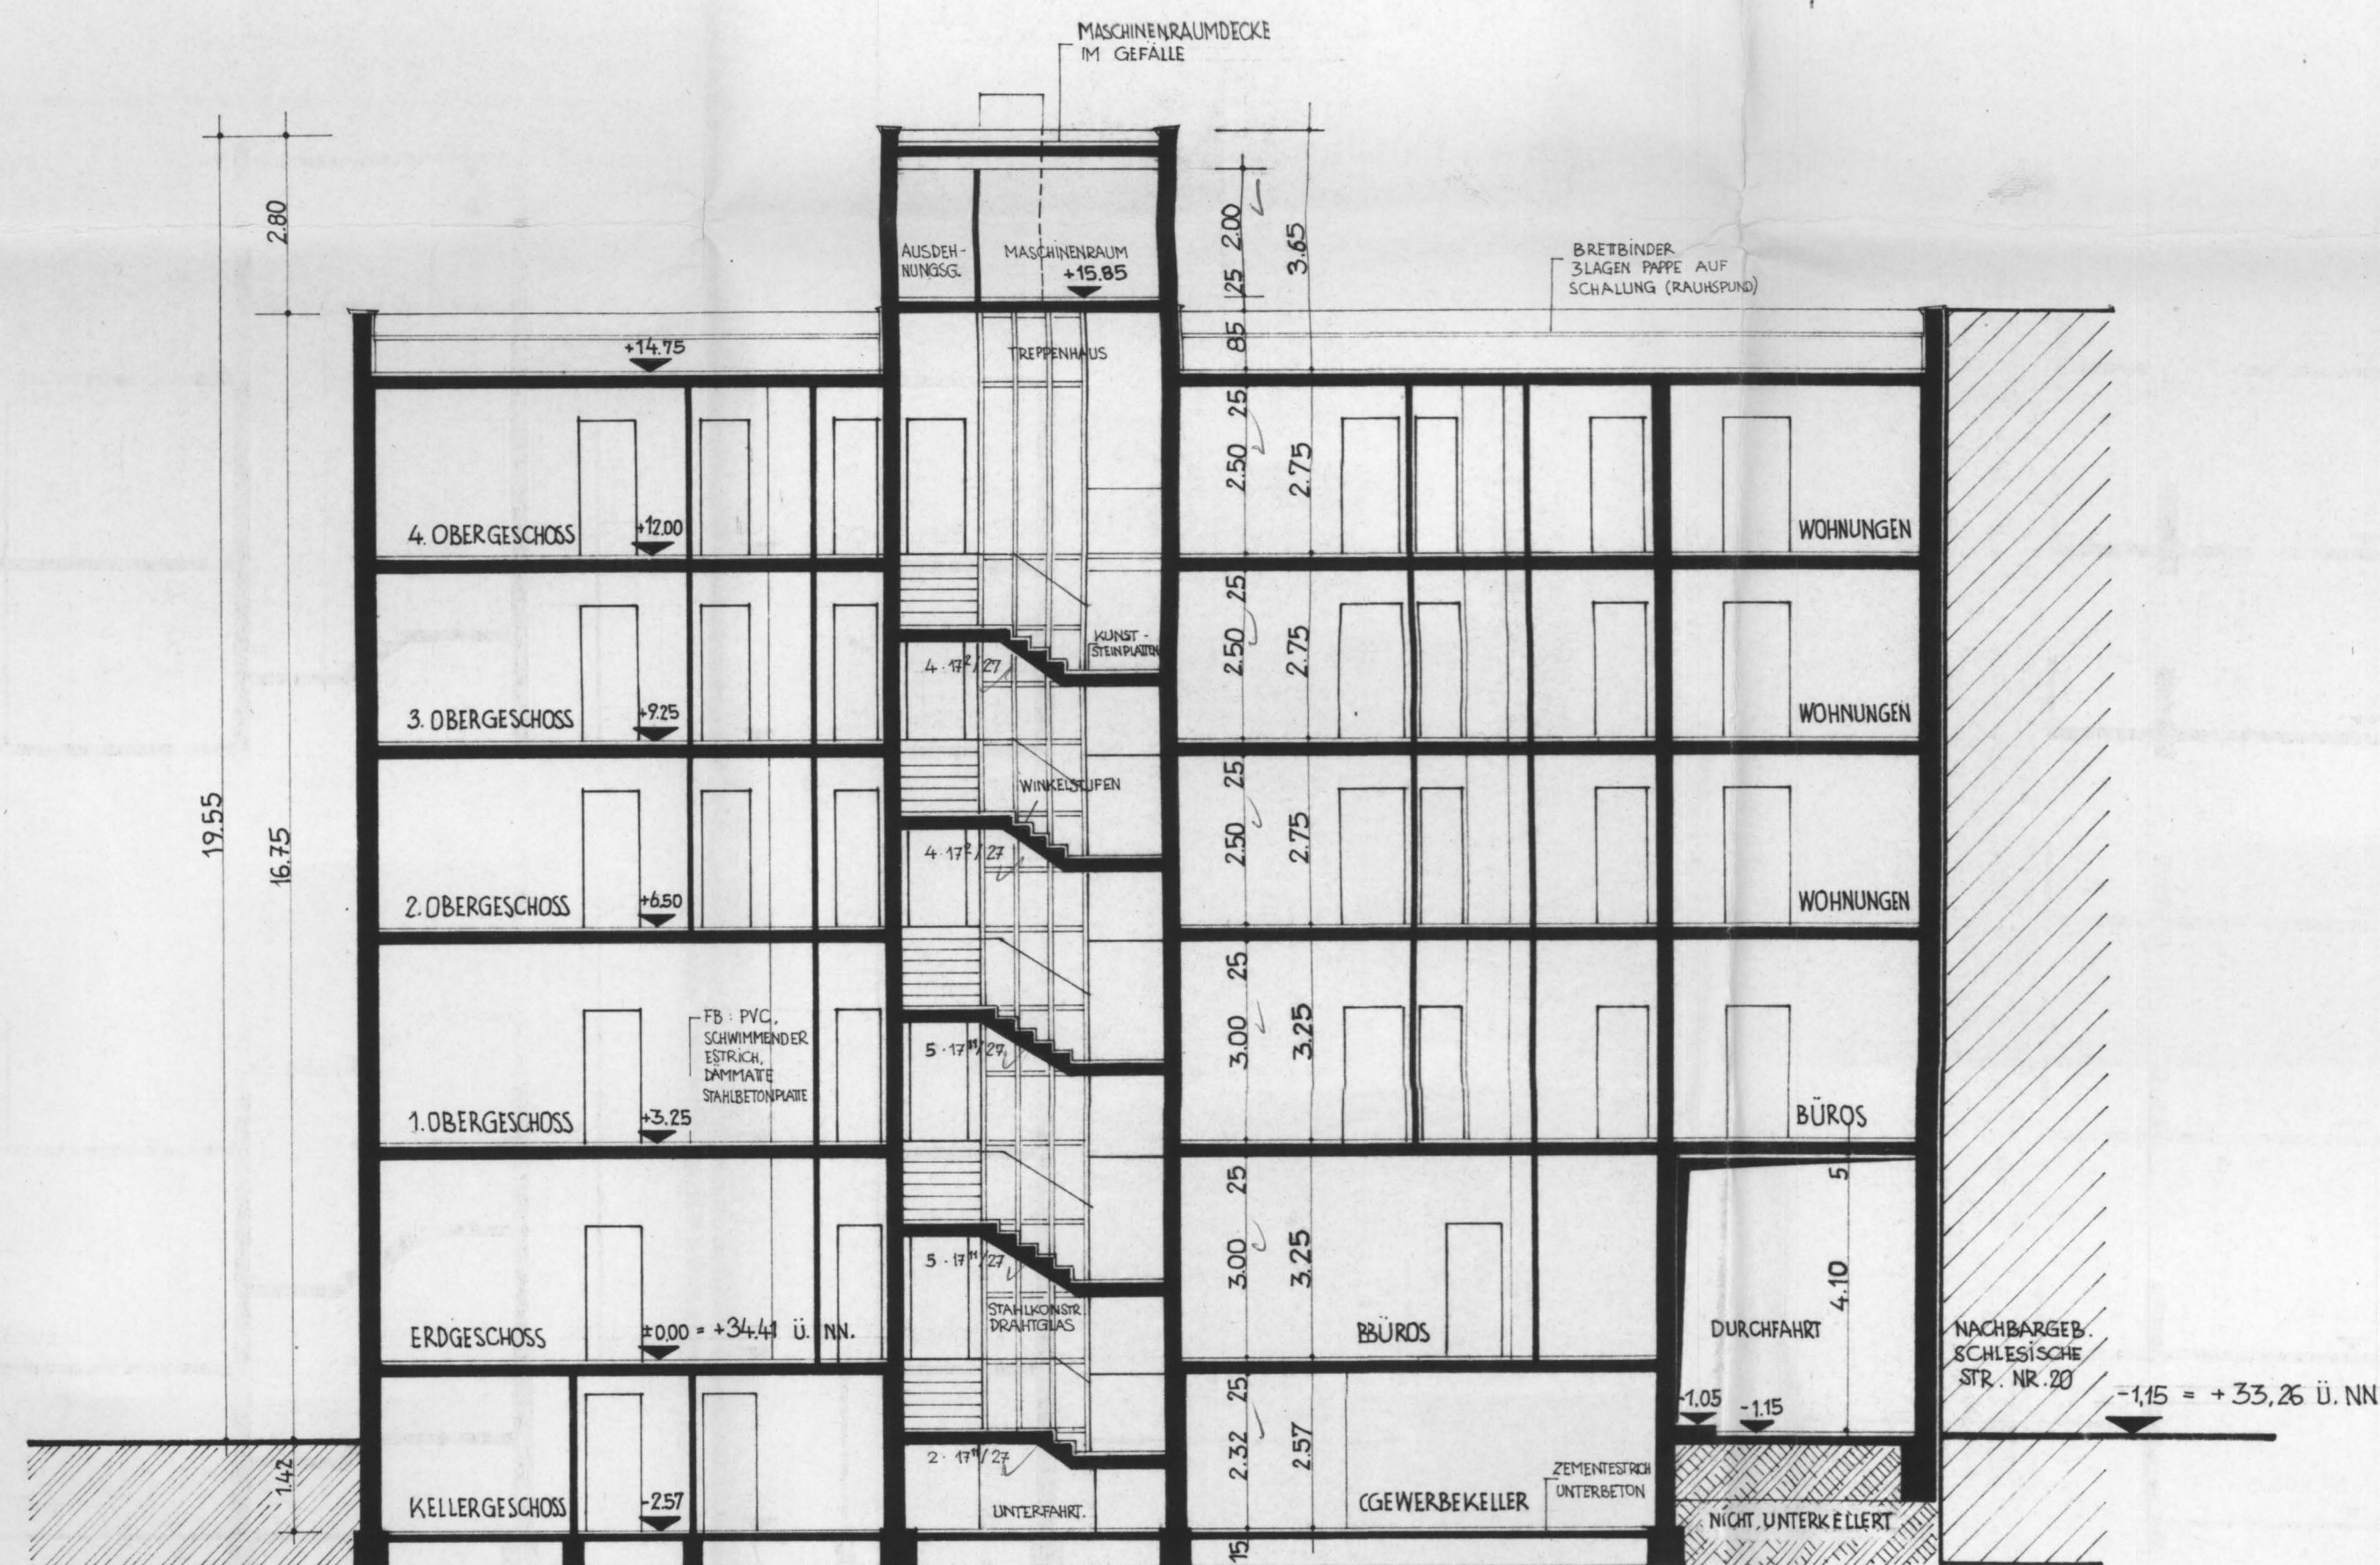

LÄNGSSCHNITT A-B

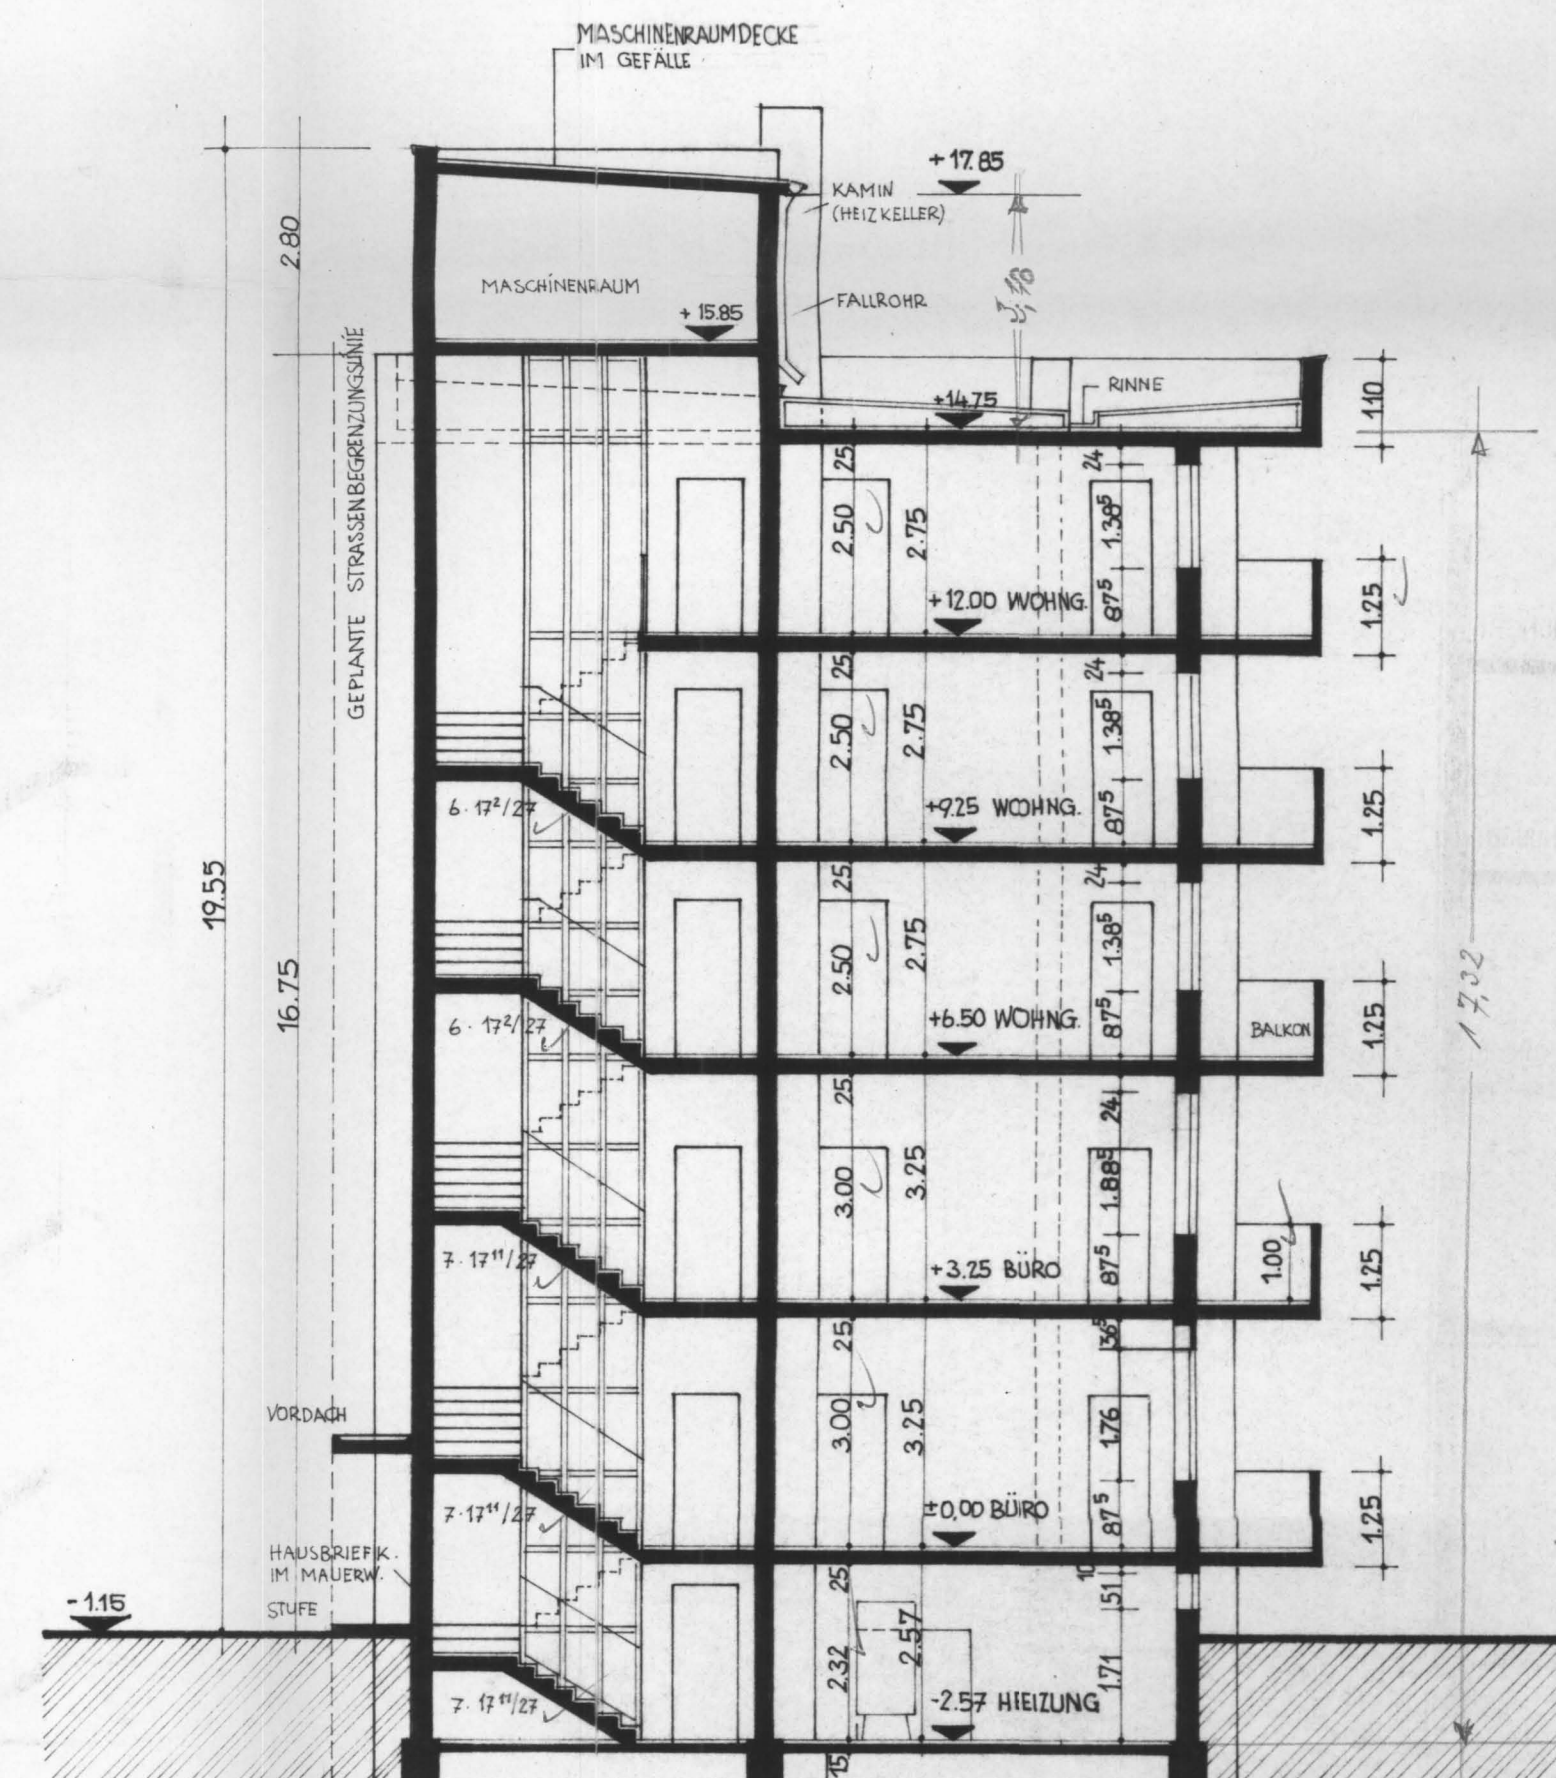

QUERSCHNITT C-D